

المحافظة : الدقهلية

المركز : المنصورة

المدينة / القرية : مدينة المنصورة

حوض الساحل القبلى نمرة 12 جزاير فصل ثالث+حوض الحوشه نمرة 72 جزاير فصل اول

حوض الساحل القبلى نمرة 12 جزاير فصل ثالث


رقم الموقع : MNR626

اسم المنتفع : / الادارة العامة لصرف شمال الدقهليه ووسط الدقهليه

ملاحظات :

تاريخ الطباعة : 4/30/2024

تمت أعمال الرفع المساحي للتواجدات طبقا لقرار اللجنة رقم 198 لسنة 2023م
(اللجنة الفنية القانونية المالية لاستلام جميع الاراضي والعقارات والبيانات . المستندات الخاصة بالاراضي التي الت ولايتها .وزارة الموارد المائية والري بموجب القانون رقم 147 لسنة 2021مبارشة ممثلي إدارة عملية النيل - هيئة التسيير و التنمية الزراعية - الاصلاح الزراعي تم إدراج تجزئات أراضي طرح النهر طبقا لما هو وارد من مديرية المساحة)
تم تحديد قطع الاملاك وإدراج مسطحاتها بناءاً علي البحث الوارد من مصلحة الشهر العقاري
أراضي خارج الحياض طبقاً لبحث الشهر العقاري هي طرح نهر أملاك دولة وفقاً للقانون رقم 147 لسنة 2021 م بإصدار قانون الموارد المائية و الري في المادة الثانية الفقرة رقم 1

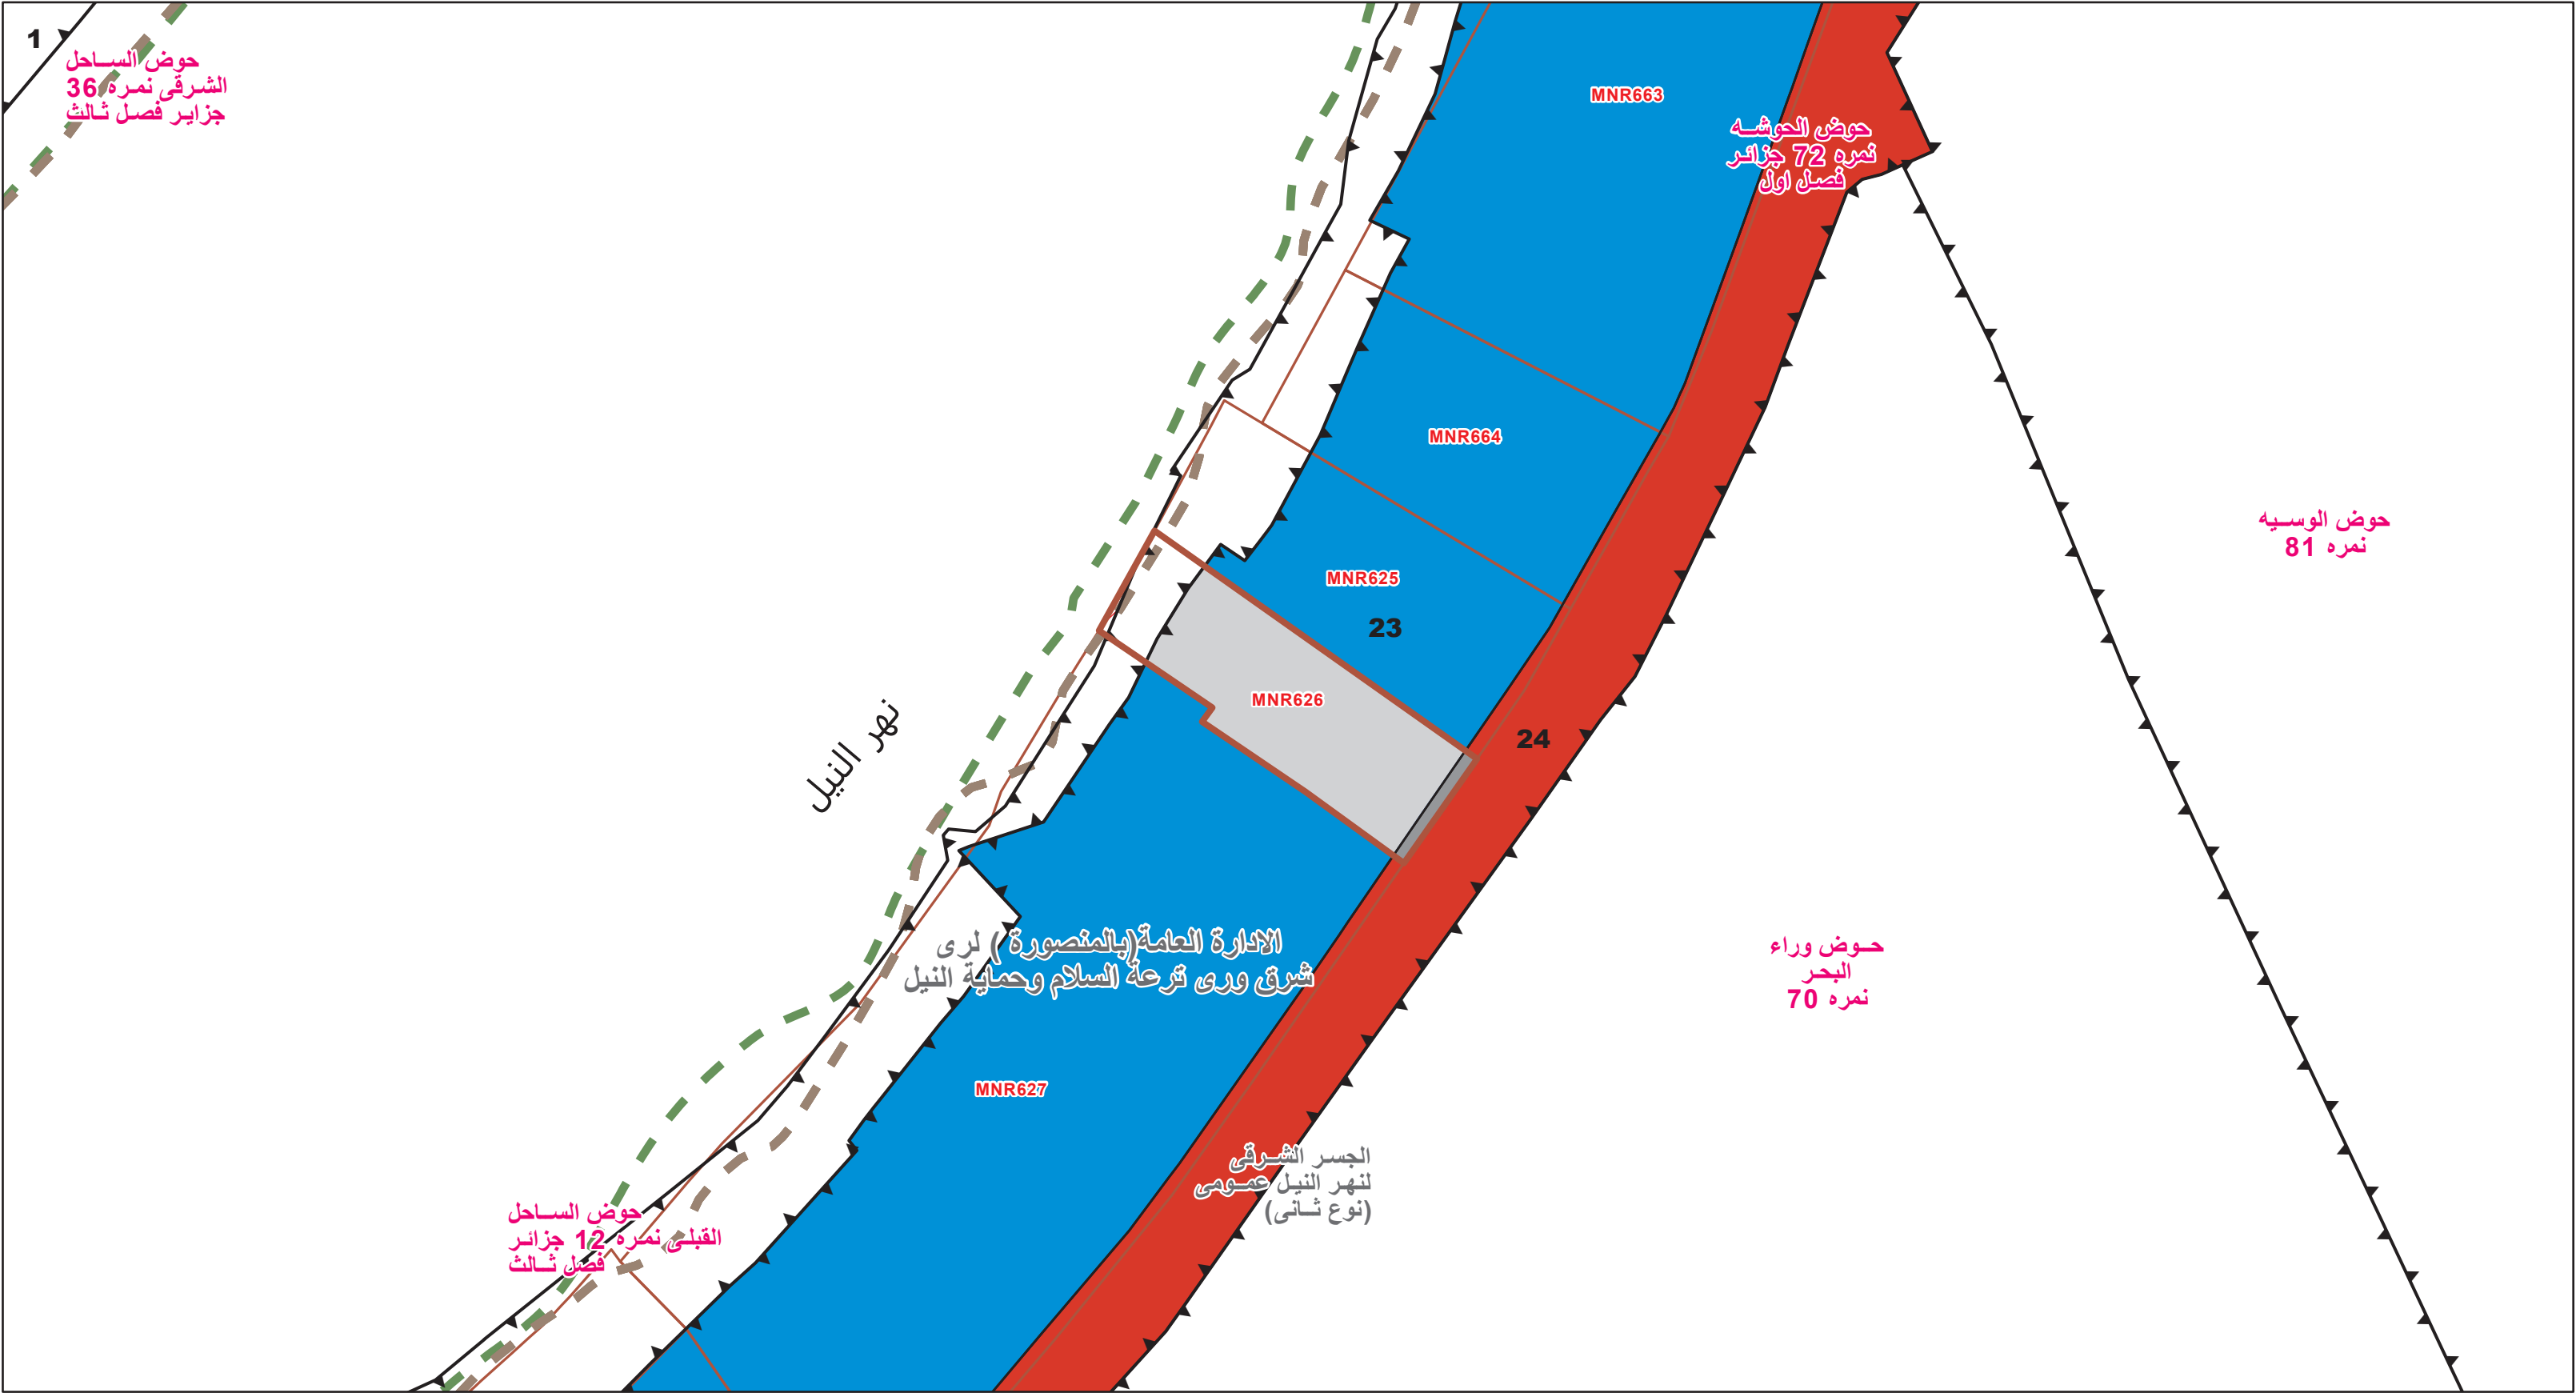

جدول بيانات املاك الدولة										مسطح استمارة 300		مسطح الاملاك				اسم الجهة	اسم المالك	رقم القطعة	اسم الحوض	اسم القرية / المدينة	الرمز
س	ط	ف	م	س	ط	ف	م	س	ط	ف	م	س	ط	ف	م						
												2.2	0	0	15.82						MNR626
طبقا للقانون رقم 147 لسنة 2021م بإصدار قانون الموارد المائية و الري في المادة الثانية الفقرة رقم 1 هي املاك دولة																	املاك اميرية				

جمهورية مصر العربية

وزارة الموارد المائية و الري

الهيئة المصرية العامة للمساحة

EGYPTIAN SURVEY AUTHORITY

أنتجت بمعرفة : الادارة المركزية للسجل العيني

بناءاً على البيانات الواردة من مديرية المساحة

جدول مسطحات التواجد بالمتر المربع

إجمالي مسطح التواجد	1864.12
مسطح الاراضي خارج الحياض	15.82
مسطح التعدي علي جسر نهر النيل	68.41
مسطح التعدي علي المنافع العامة	1542.12
مسطح التعدي علي الشارع	
مسطح المنشآت داخل التواجد	
مسطح الردم واجب إزالته طبقا لخرائط معهد البحوث لسنة 1982م	40.34
مسطح الردم واجب إزالته طبقا لخرائط معهد البحوث لسنة 2003م	0.00

الاحداثيات الخاصة بالموقع طبقا للاحداثي العالمي WGS_1984_UTM_Zone_36N

رقم الموقع	E	N
MNR626	31° 23' 50.267" E	31° 3' 15.639" N

الرموز و الاصطلاحات المساحية

نقطة احداثي

حد الملكية

حد حوض

حد قرية

خط التهذيب طبقا لاحداثيات معهد بحوث النيل خرائط 1982 م

خط موازي لخط التهذيب1982 م على بعد 30 م

خط موازي لجسر نهر النيل على مسافة 30م

خط الشاطئ طبقا لاحداثيات معهد بحوث النيل خرائط 1982م

خط الشاطئ طبقا لاحداثيات معهد بحوث النيل خرائط 2003م

اراضي الرفع بالطبيعة (التواجدات)

مياشي رفع بالطبيعة

تجزئات تاريخية

تجزئات مؤقتة

جسر نهر النيل

الطريق

مشروعات المنفعة العامة (الري)

مشروعات المنفعة العامة (الصرف)

مشروعات المنفعة العامة (اخرى)

اراضي خارج الحياض (ارساب)

التعدي علي المنفعة العامة

التعدي علي جسر نهر النيل

الردم لسنة 1982م

مياشي رفع القوات المسلحة

املاك الاوقاف

املاك اميرية

اصلاح زراعي

تأشيرة تحفظ

املاك اخصري

طول الواجبة علي النيل

22.68

نقطة احداثي