

المركز : المنصورة

تاريخ الطباعة : 4/30/2024



تمت أعمال ارض المساحي الجوفات لتحتاج ارض للبيجة رقم 198 لسنة 2023م
 (البيجة التوفيقية التامة لاصلاح جميع الاراضي والغلات والبساتين والمستندات الخاصة بالاراضي التي التاها لوزارة الموارد
 المائية والري بموجب القانون رقم 147 لسنة 2021م) وان كان متملي ارض البيجة الحالية - هيئة التعمير والتعمية الزراعية - اصلاح الزراعي
 تم ادراجه تحت اراضي طرح شهر ميقيا لما هو وارد من مديرية المساحة)

تم تحديد قطع الاملاك واخراج مساحاتها بناءاً على البحث الوارد من مصلحة الشهر العقاري
 اراضي حدار الجنيح لبيجة لحقل الشهر العقاري هي طرح ارض املاك دولة وفقاً للقانون رقم 147 لسنة 2021م بصنادار القارة المادية والري
 في المدة الموقعة رقم 1

اسم المنتفع : / وزاره الري

ملاحظات :

الهيئة المصرية العامة للمساحة



EGYPTIAN SURVEY AUTHORITY

بناءً على البيانات الواردة من مديرية المساحة

جدول مسطحات التواجد بالمتر المربع



1677.49	إجمالي مسطح التواجد
	مسطح الاراضي خارج الحياض
84.79	مسطح التهدي علي جسر نهر النيل
1592.71	مسطح التهدي علي المنافع العامة
	مسطح التهدي علي الشارع
	مسطح المنشآت داخل التواجد
0.00	مسطح الردم واجب ازالته طبقا لخرائط معهد البحوث لسنة 1982م
0.00	مسطح الردم واجب ازالته طبقا لخرائط معهد البحوث لسنة 2003م

لاحداثيات الخاصة بالموقع طبقا للاحداثي العالمي WGS_1984_UTM_Zone_36N

N	E	رقم الموقع
31° 3' 10.548" N	31° 23' 46.021" E	MNR628

لرموز و الاصطلاحات المساحية

نقطة اعدادي	حد الملكية	حد حوض	حد قرية
حد مركز			
حد محافظة			
حد نهر النيل			
خط التهذيب طبقا لاحداثيات معهد بحوث النيل خرائط 1982 م			
خط موازي لخط التهذيب 1982 م على بعد 30 م			
خط موازي لجسر نهر النيل على مسافة 30م			
خط الشاطئ طبقا لاحداثيات معهد بحوث النيل خرائط 1982م			
خط الشاطئ طبقا لاحداثيات معهد بحوث النيل خرائط 2003م			
اراضي الرفع الطبيعية (التواجدات)			
اراضي خارج الحياض (ارساب)			
مباني رفع الطبيعة			
مباني رفع الطبيعة			
تجزئات تاريخية			
تجزئات تاريخية			
تجزئات موقنة			
تجزئات موقنة			
مباني رفع القوات المسلحة			
مباني رفع القوات المسلحة			
املاك الاوقاف			
املاك الاوقاف			
املاك اميرية			
املاك اميرية			
اصلاح زراعى			
اصلاح زراعى			
تأسيسية تحفظ			
تأسيسية تحفظ			
املاك اخري			
املاك اخري			

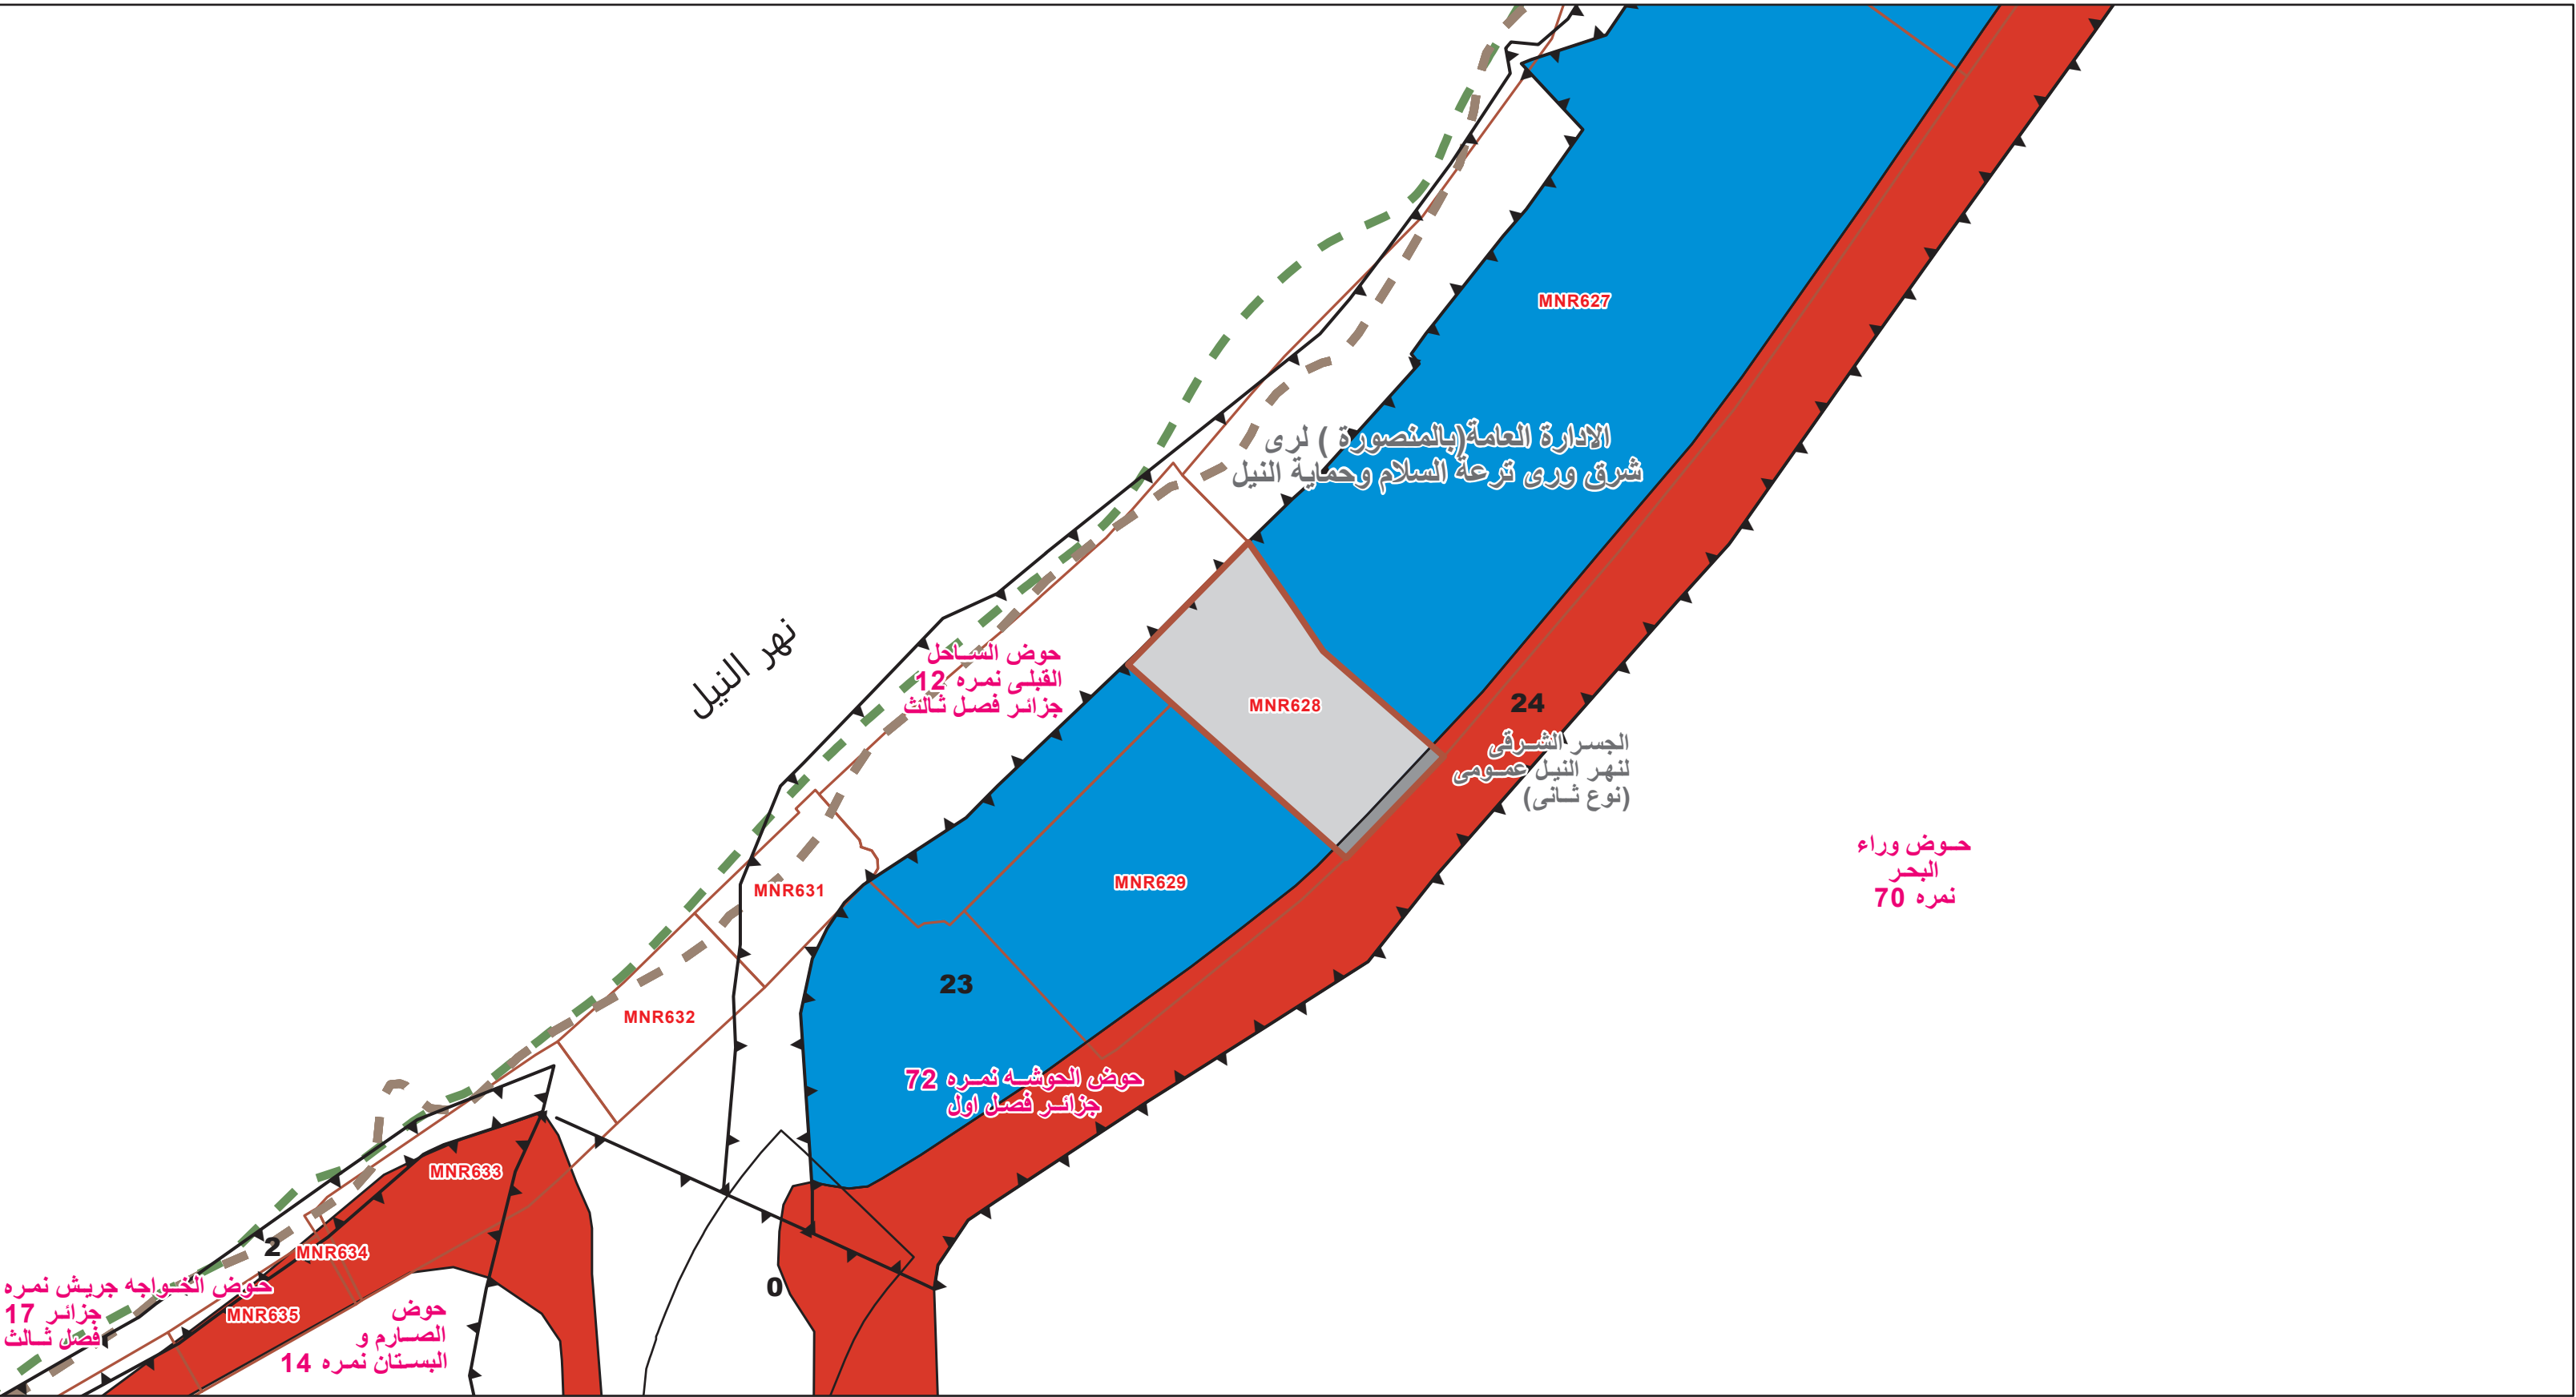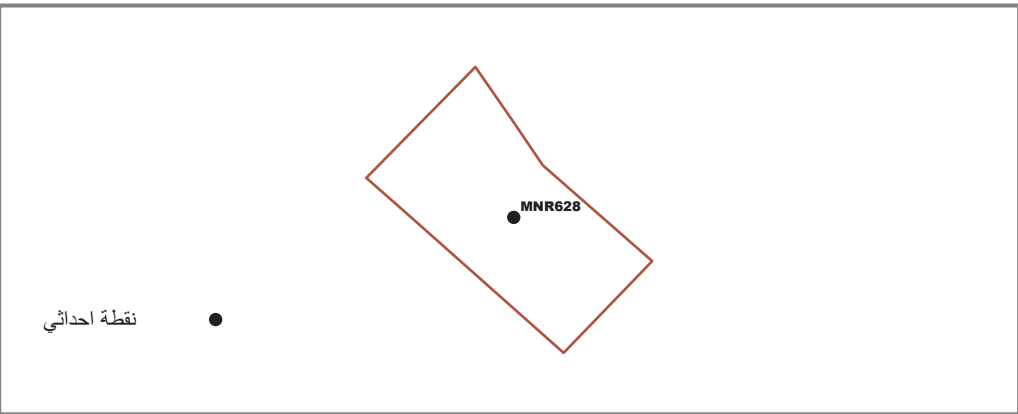

جدول بيانات املاك الدولة

جدول بيانات املاك الدولة														
مسطح الجزء المتداخل بالتواجد 2م		مسطح الاملاك				مسطح استمارة 300				اسم الجهة	اسم المالك	رقم القطعة	اسم الحوض	الرمز
		م 2	ف	ط	س	م 2	ف	ط	س					
		موقف الاملاك												