

تاريخ الطباعة : 4/30/2024

خارج الأحواض

MNR657 : رقم الموقع

اسم المنتفع : / نادي التجديف لضباط الشرطة يوجد به 7 مباني

ملاحظات :

جمهورية مصر العربية

وزارة الموارد المائية و الري

الهيئة المصرية العامة للمساحة



EGYPTIAN SURVEY AUTHORITY

أنتجت بمعرفة : الادارة المركزية للسجل العيني

بناءً على البيانات الواردة من مديرية المساحة

جدول مسطحات التواجد بالمتر المربع

19134.88	إجمالي مسطح التواجد
19134.88	مسطح الاراضي خارج الحياض
	مسطح التعدي علي جسر نهر النيل
	مسطح التعدي علي المنافع العامة
	مسطح التعدي علي الشارع
	مسطح المنشآت داخل التواجد
16318.20	مسطح الردم واجب ازالته طبقا لخرائط معهد البحوث لسنة 1982م
98.83	مسطح الردم واجب ازالته طبقا لخرائط معهد البحوث لسنة 2003م

لاحداثيات الخاصة بالموقع طبقا للاحداثي العالمي WGS_1984_UTM_Zone_36N

N	E	رقم الموقع
31° 2' 48.093" N	31° 21' 24.117" E	MNR657


الرموز و الاصطلاحات المساحية

نقطة اعدادي	●
حد الملكية	—
حد حوض	▲▼
حد قرية	●—●
خط التهذيب طبقا لاحداثيات معهد بحوث النيل خرائط 1982 م	■ ■ ■ ■ ■
خط موازي لخط التهذيب 1982 م على بعد 30 م	- - - - -
خط موازي لجسر نهر النيل على مسافة 30م	- - - - -
خط الشاطئ طبقا لاحداثيات معهد بحوث النيل خرائط 1982م	■ ■ ■ ■ ■
خط الشاطئ طبقا لاحداثيات معهد بحوث النيل خرائط 2003م	■ ■ ■ ■ ■
اراضي الرفع بالطبيعة (التواجدات)	□
مبانى رفع بالطبيعة	□
تجزئات تاريخية	□
تجزئات مؤقتة	□
جسر نهر النيل	□
الطـــــــــــــــــرق	□
مشروعات المنفعة العامة (السري)	□
مشروعات المنفعة العامة (الصرف)	□
مشروعات المنفعة العامة (اخرى)	□
ارضى خارج الحياض (ارساب)	□
التعدي على المنفعة العامة	□
التعدي على جسر نهر النيل	□
الردم لمسئنة 1982م	□
مبانى رفع القوات المسلحة	□
املاك الاوقاف	□
املاك امـــــــــــــــــيرية	□
اصلاح زراــــــــــــــــعى	□
تأشيرة تحفــــــــظ	□
املاك اخــــــــــــــــري	□

طول الواجبة على الفيل

376.47

نقطة احداثي

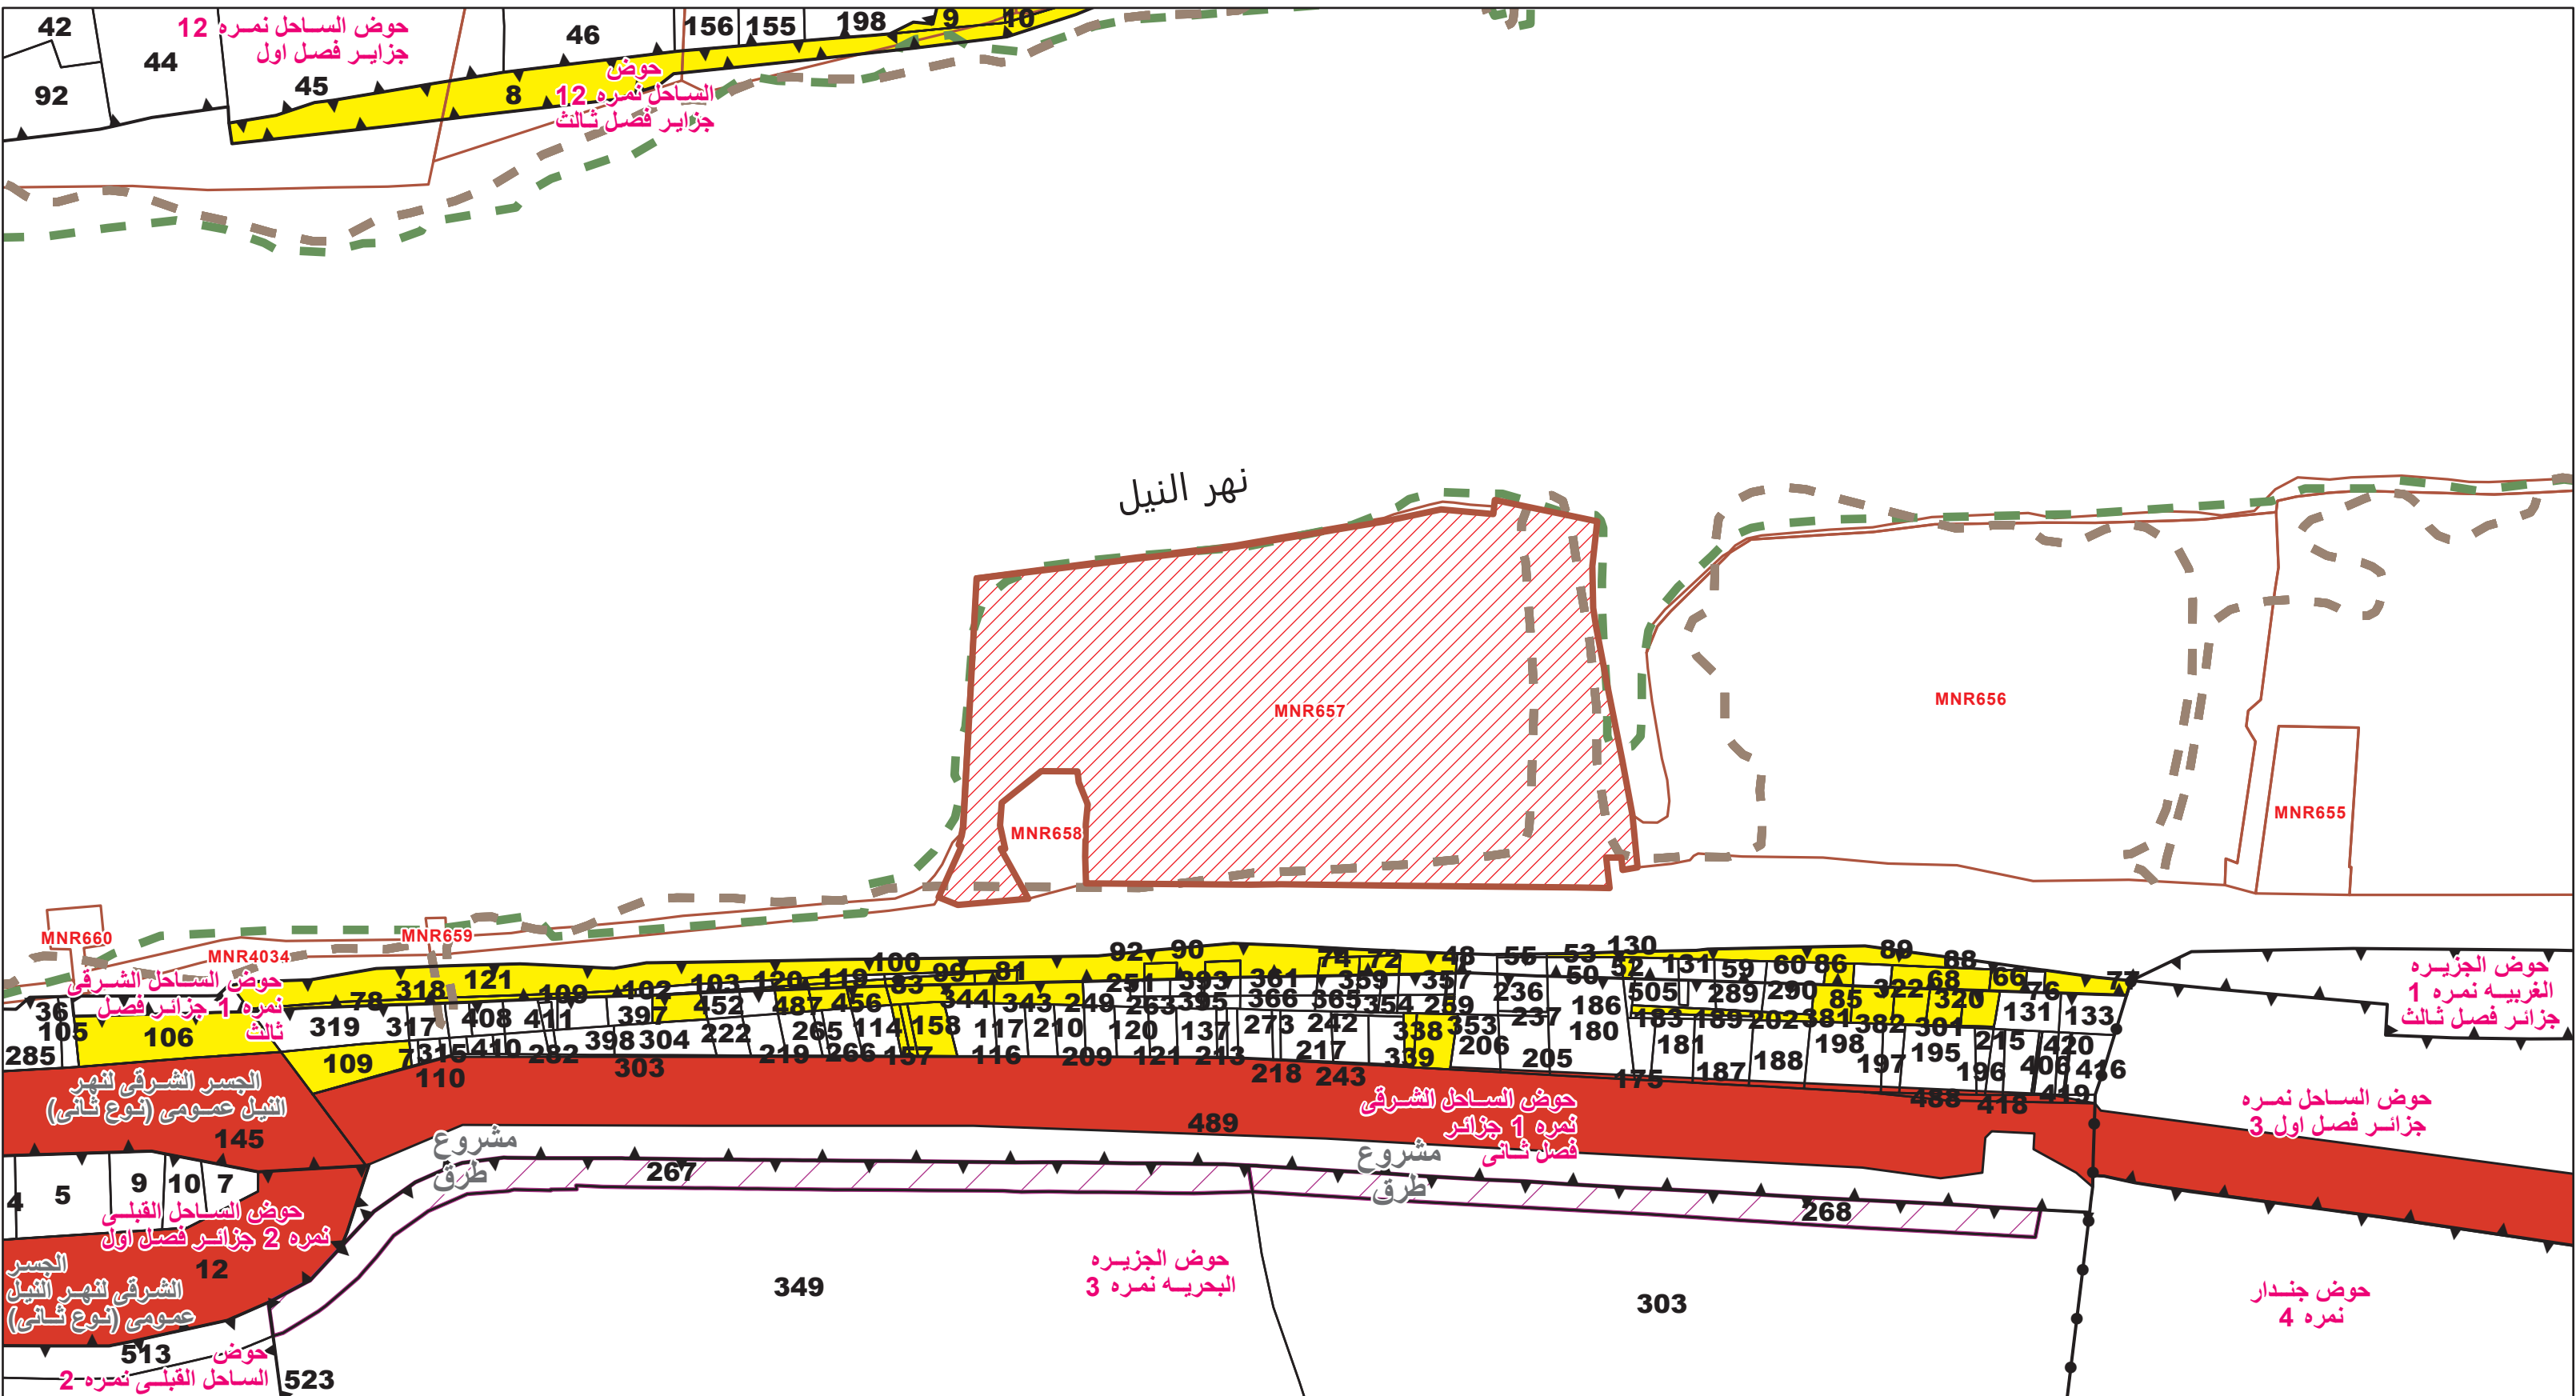

جدول بيانات املاك الدولة

جدول بيانات املاك الدولة															
		مسطح الاملاك				مسطح استثمارة 300									
الرمز	اسم القرية / المدينة	اسم الحوض	رقم القطعة	اسم المالك	اسم الجهة	س	ط	ف	م 2	س	ط	ف	م 2	موقف الاملاك	مسطح الجزء المتداخل بالتواجد م2
MNR657				طبقا للقانون رقم 147 لسنة 2021م بإصدار قانون الموارد المائية و الري في المادة الثانية الفقرة رقم 1 هي املاك دولة	املاك اميرية					7.7	13	4	19134.86		19134.88