

المحافظة : الدقهلية

المركز : المنصورة

المدينة / القرية : مدينة المنصورة

تاريخ الطباعة : 4/30/2024


خارج الأحواض

رقم الموقع : MNR660

اسم المتنفع : مرسى بيراميزا ستار

ملاحظات :

تمت أعمال الرفع المساحي للتواجدات طبقاً لقرار اللجنة رقم 198 لسنة 2023م
(اللجنة الفنية القانونية المالية لاستلام جميع الأراضي والعقارات والبيانات . والمستندات الخاصة بالأراضي التي ألت ولايتها لوزارة الموارد المائية والري بموجب القانون رقم 147 لسنة 2021م بإشراف ممثلي إدارة عملية النيل - هيئة التسيير و التنمية الزراعية - الإصلاح الزراعي تم إدراج تجزئات أراضي طرح النهر طبقاً لما هو وارد من مديرية المساحة)
تم تحديد قطع الأملاك وإدراج مسطحاتها بناءً على البحث الوارد من مصلحة الشهر العقاري
أراضي خارج الحياض طبقاً لبحث الشهر العقاري هي طرح نهر أملاك دولة وفقاً للقانون رقم 147 لسنة 2021 م بإصدار قانون الموارد المائية و الري في المادة الثانية الفقرة رقم 1

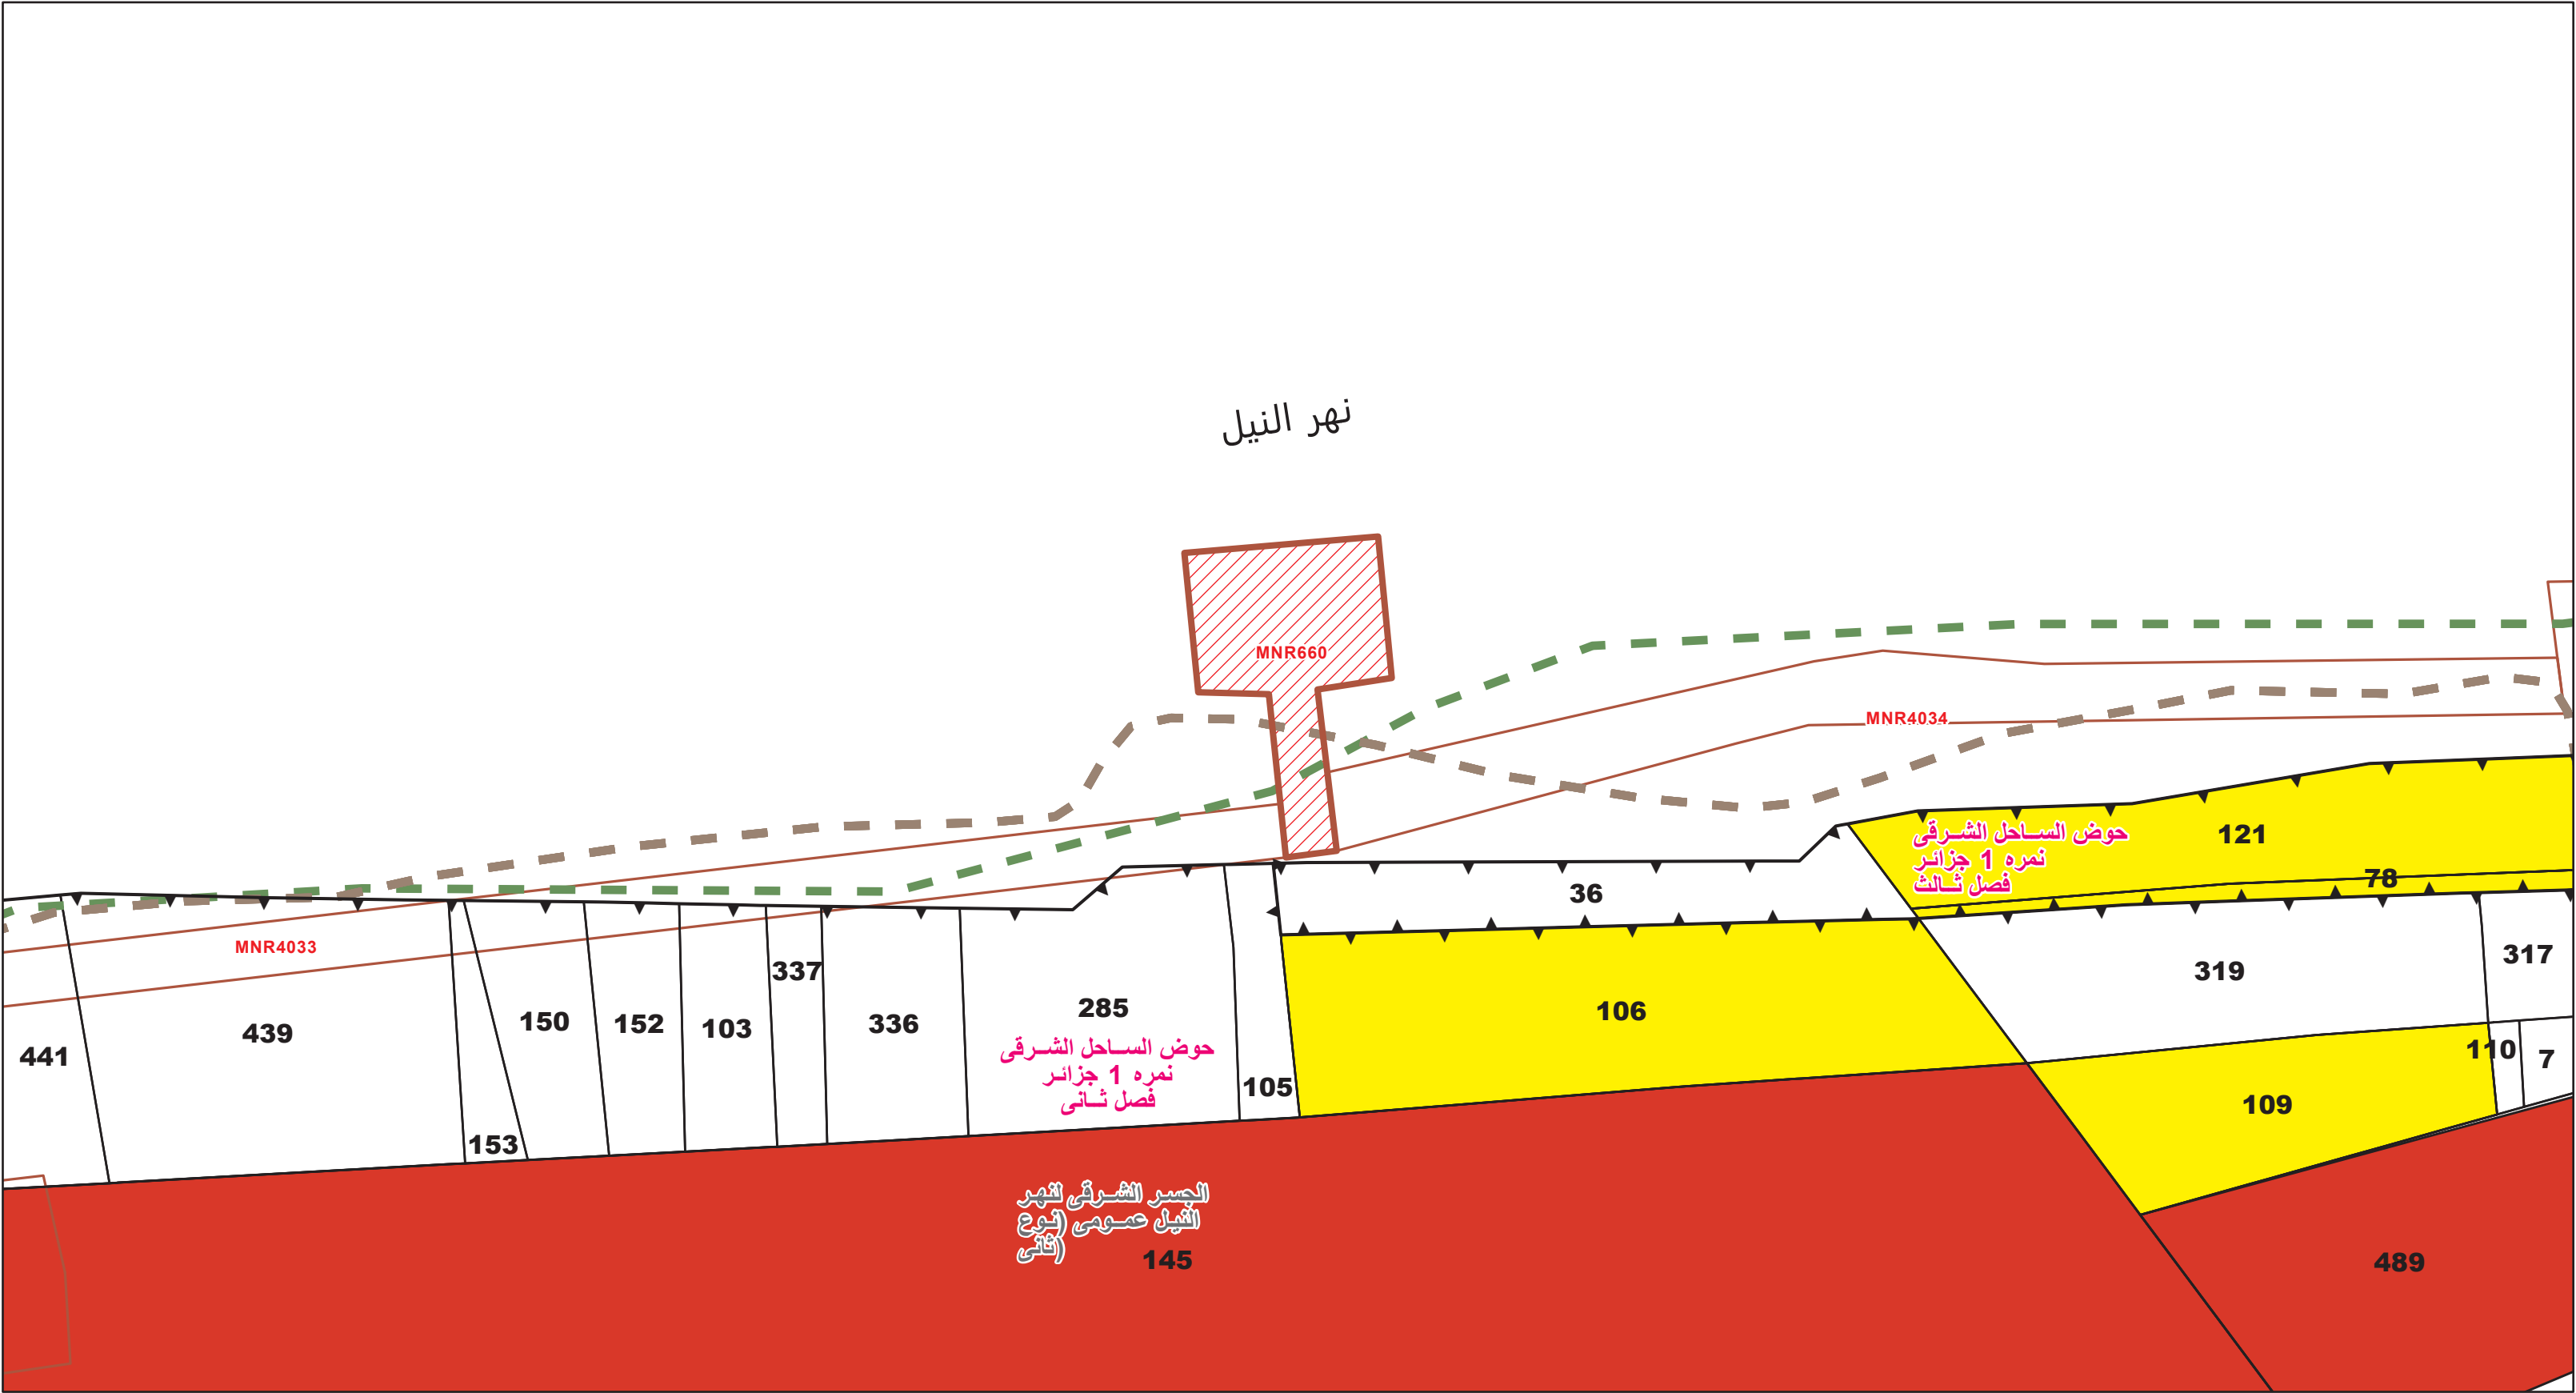

جدول بيانات املاك الدولة										مسطح استمارة 300		مسطح الاملاك				الرمز	اسم القرية / المدينة	اسم الحوض	رقم القطعة	اسم المالك	اسم الجهة	مس	ط	ف	م 2	موقف الاملاك	مسطح الجزء المتداخل بالتواجد م2
										س	ط	ف	م 2	س	ط	ف	م 2										
MNR660														10.1	1	0	248.41				املاك اميرية	طبقا للقانون رقم 147 لسنة 2021م بإصدار قانون الموارد المائية و الري في المادة الثانية الفقرة رقم 1 هي املاك دولة					

جمهورية مصر العربية
وزارة الموارد المائية و الري
الهيئة المصرية العامة للمساحة

EGYPTIAN SURVEY AUTHORITY

أنتجت بمعرفة : الادارة المركزية للسجل العيني

بناءً على البيانات الواردة من مديرية المساحة

جدول مسطحات التواجد بالمتر المربع

إجمالي مسطح التواجد	248.41
مسطح الاراضي خارج الحياض	248.41
مسطح التعدي علي جسر نهر النيل	
مسطح التعدي علي المنافع العامة	
مسطح التعدي علي الشارع	
مسطح المنشآت داخل التواجد	
مسطح الردم واجب إزالته طبقا لخرائط معهد البحوث لسنة 1982م	205.59
مسطح الردم واجب إزالته طبقا لخرائط معهد البحوث لسنة 2003م	220.83

الاحداثيات الخاصة بالموقع طبقا للاحداثي العالمي WGS_1984_UTM_Zone_36N

رقم الموقع	E	N
MNR660	31° 21' 10.270" E	31° 2' 45.939" N

الرموز و الاصطلاحات المساحية

نقطة احداثي

حد الملكية

حد حوض

حد قرية

خط التهذيب طبقا لاحداثيات معهد بحوث النيل خرائط 1982 م

خط موازي لخط التهذيب 1982 م على بعد 30 م

خط موازي لجسر نهر النيل على مسافة 30م

خط الشاطئ طبقا لاحداثيات معهد بحوث النيل خرائط 1982م

خط الشاطئ طبقا لاحداثيات معهد بحوث النيل خرائط 2003م

اراضي الرفع بالطبيعة (التواجدات)

مياقي رفع بالطبيعة

تجزئات تاريخية

تجزئات مؤقتة

جسر نهر النيل

الطريق

مشروعات المنفعة العامة (الري)

مشروعات المنفعة العامة (الصرف)

مشروعات المنفعة العامة (اخرى)

اراضي خارج الحياض (ارساب)

التعدي علي المنفعة العامة

التعدي علي جسر نهر النيل

الردم لسنة 1982م

مياقي رفع القوات المسلحة

املاك الاوقاف

املاك اميرية

اصلاح زراعي

تأشيرة تحفظ

املاك اخصري

طول الواجهة علي النيل

67.48

نقطة احداثي