المحافظـة : الدقهلية المـركـــز : المنصورة المدينة / القرية : ميت بدر خميس

حوض الساحل الوسطانى نمره 8 جزائر فصل اول+حوض الساحل الوسطانى نمره 8 جزائر فصل ثالث

رقم الموقع : MNR754

اسم المنتفع : / ورثه فتح الله شعبان عبدالرحيم -ومصطفي فراج له 4 قيراط

ملاحظات :

تاريخ الطباعة : 15-04-2026

تمت أعمال الرفع المساحي للتواجدات طبقا لقرار اللجنة رقم 198 لسنة 2023م
(اللجنة الفنية القانونية المالية لأستلام جميع الاراضي والعقارات والبيانات والمستندات الخاصة بالاراضي التي آلت ولايتها لوزارة الموارد المائية والري بموجب القانون رقم 147 لسنة 2021وبارشاد ممثلي إدارة حماية النيل - هيئة التعمير و التنمية الزراعية - الاصلاح الزراعي تم إدارج تجزئات أراضي طرح للنهر طبقا لما هو وارد من مديرية المساحة)

تم تحديد قطع الاملاك وإدراج مسطحاتها بناءاً على البحث الوارد من مصلحة الشهر العقاري
أراضي خارج الحياض طبقا لبحث الشهر العقاري هي طرح نهر أملاك دولة وفقا للقانون رقم 147 لسنة 2021 م بإصدار قانون الموارد المائية و الري في المادة الثانية الفقرة رقم ا

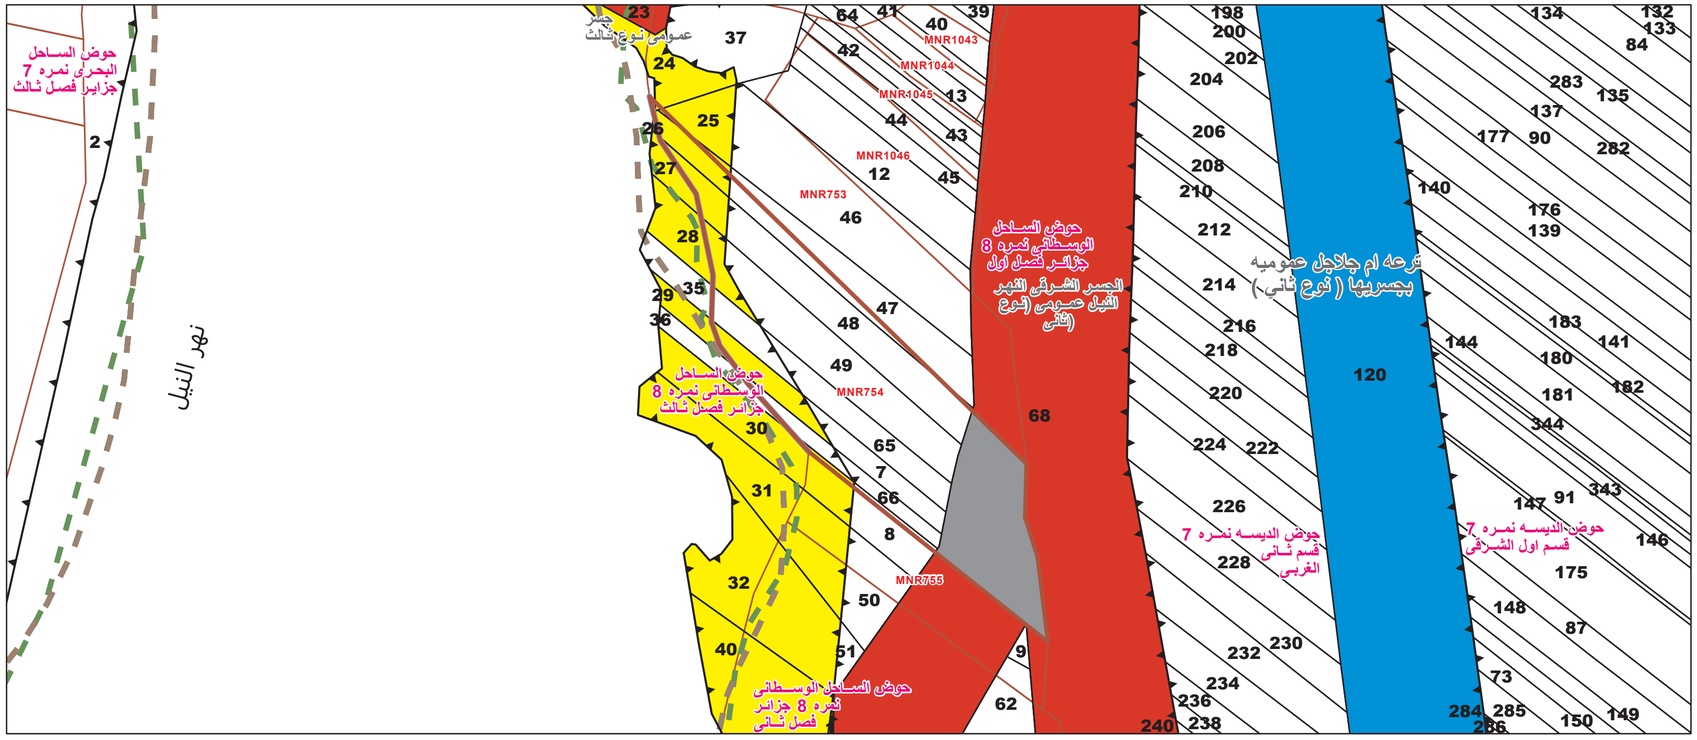

جدول بيانات املاك الدولة

الرمز	اسم القرية / المدينة	اسم الحوض	رقم القطعة	اسم المالك	اسم الجهة	مسطح استمارة 300 س	مسطح استمارة 300 ط	مسطح استمارة 300 ف	مسطح استمارة 300 م 2	مسطح الاملاك س	مسطح الاملاك ط	مسطح الاملاك ف	مسطح الاملاك م 2	موقف الاملاك	مسطح الجزء المتداخل بالتواجد م2
MNR754				طبقا للقانون رقم 147 لسنة 2021م بإصدار قانون الموارد المائية و الري في المادة الثانية الفقرة رقم 1 هى املاك دولة	املاك اميرية					0.2	0	0	1.74		1.74
MNR754	ميت بدر خميس	حوض الساحل الوسطانى نمره 8 جزائر فصل ثالث	24	اطيان اميريه	املاك اميرية	1.0	1	0	182.33	3.0	0	0	21.88	مشاع	1.27
MNR754	ميت بدر خميس	حوض الساحل الوسطانى نمره 8 جزائر فصل ثالث	25	اطيان اميريه	املاك اميرية	16.0	0	0	116.69	16.0	0	0	116.69	كامل	2.76
MNR754	ميت بدر خميس	حوض الساحل الوسطانى نمره 8 جزائر فصل ثالث	26	اطيان اميريه	املاك اميرية	13.0	0	0	94.81	13.0	0	0	94.81	كامل	78.10
MNR754	ميت بدر خميس	حوض الساحل الوسطانى نمره 8 جزائر فصل ثالث	27	اطيان اميريه	املاك اميرية	17.0	0	0	123.98	17.0	0	0	123.98	كامل	74.37
MNR754	ميت بدر خميس	حوض الساحل الوسطانى نمره 8 جزائر فصل ثالث	28	اطيان اميريه	املاك اميرية	3.0	1	0	196.91	3.0	1	0	196.91	كامل	62.41
MNR754	ميت بدر خميس	حوض الساحل الوسطانى نمره 8 جزائر فصل ثالث	29	اطيان اميريه	املاك اميرية	1.0	1	0	182.33	12.0	0	0	87.52	مشاع	111.57
MNR754	ميت بدر خميس	حوض الساحل الوسطانى نمره 8 جزائر فصل ثالث	30	اطيان اميريه	املاك اميرية	10.0	2	0	423.00	22.0	1	0	335.48	مشاع	12.00

جمهورية مصر العربية
وزارة الموارد المائية و الري
الهيئة المصرية العامة للمساحة

EGYPTIAN SURVEY AUTHORITY

أنتجت بمعرفة : الادارة المركزية للسجل العيني

بناءاً على البيانات الواردة من مديرية المساحة

جدول مسطحات التواجد بالمتر المربع

إجمالي مسطح التواجد	2533.57
مسطح الاراضي خارج الحياض	1.74
مسطح التعدي علي جسر نهر النيل	554.89
مسطح التعدي علي المنافع العامة	
مسطح التعدي علي الشارع	
مسطح المنشأت داخل التواجد	
مسطح الردم واجب إزالته طبقا لخرائط معهد البحوث لسنة 1982م	0.00
مسطح الردم واجب إزالته طبقا لخرائط معهد البحوث لسنة 2003م	0.00

الاحداثيات الخاصة بالموقع طبقا للاحداثي العالمي WGS_1984_UTM_Zone_36N

رقم الموقع	E	N
MNR754	31° 20' 14.611" E	31° 1' 37.099" N

الرموز و الاصطلاحات المساحية

- نقطة احداثي
- حد الملكية
- حد مـــركز
- حد حوض
- حد محافظة
- حد قرية
- حد نهر النيل
- خط التهذيب طبقا لاحداثيات معهد بحوث النيل خرائط 1982 م
- خـــط مـــوازي لخـــط التهـذيب1982 م علـــى بعد 30 م
- خـــط مـــوازي لجـــسر نهـــر النيـــل على مسافة 30م
- خط الشاطئ طبقا لاحداثيات معهد بحوث النيل خرائط 1982م
- خط الشاطئ طبقا لاحداثيات معهد بحوث النيل خرائط 2003م
- اراضـــي الرفع بالطبيعة (التواجدات)
- اراضـــي خارج الحياض (ارساب)
- مبانـــي رفـــع بالطبيعة
- التعدي علي المنفعة العامـة
- تـجـزئات تاريـخـيـة
- التعدي علي جسر نهر النيل
- تـجـزئات مـوقـتـة
- الـردم لـسـنـة 1982م
- جـسـر نـهـر النيل
- مبانـي رفع القوات المسلحة
- الطـــــــرق
- املاك الاوقـــــاف
- مشروعات المنفعة العامة (الـــري)
- املاك امـــــيريـــة
- مشروعات المنفعة العامة (الصـرف)
- اصلاح زراعـــــي
- مشروعات المنفعة العامة (أخـــري)
- تأشـيـرة تـــحـــفـظ
- املاك اخـــــــري

طول الواجهة علي النيل
81.39