

جمهورية مصر العربية
وزارة الموارد المائية و الري
الهيئة المصرية العامة للمساحة



بناءً على البيانات الواردة من مديرية المساحة

1261.83	إجمالي مسطح التواجد
153.89	مسطح الاراضي خارج الحياض
677.60	مسطح التcedي علي جسر نهر النيل
	مسطح التcedي علي المنافع العامة
	مسطح التcedي علي الشارع
	مسطح المنشآت داخل التواجد
470.52	مسطح الردم واجب ازالته طبقا لخرائط معهد البحوث لسنة 1982م
257.57	مسطح الردم واجب ازالته طبقا لخرائط معهد البحوث لسنة 2003م

N	E	رقم الموقع
31° 0' 25.692" N	31° 18' 27.739" E	MNR923

نقطة احداثي	حد الملكية	حد حوض	حد قرية
حد مركز			
حد محافظة			
حد نهر النيل			
خط التهذيب طبقا لاحداثيات معهد بحوث النيل خرائط 1982 م			
خط موازي لخط التهذيب 1982 م على بعد 30 م			
خط موازي لجسر نهر النيل على مسافة 30م			
خط الشاطئ طبقا لاحداثيات معهد بحوث النيل خرائط 1982م			
خط الشاطئ طبقا لاحداثيات معهد بحوث النيل خرائط 2003م			
اراضي الرفع بالطبيعة (التواجدات)			
مبانى رفع بالطبيعة			
تجزئات تاريخية			
تجزئات مؤقتة			
مبانى رفع القوات المسلحة			
الطـــــــرق			
مشروعات المنفعة العامة (السري)			
مشروعات المنفعة العامة (الصرف)			
مشروعات المنفعة العامة (اخرى)			
املاك اخصري			

56.03


نقطة احداثي

حوض قطع يوسف جزائر فصل ثالث نمرة 1 - حوض قطع يوسف جزائر فصل اول نمرة 1

MNR923 : رقم الموقع

اسم المنتفع : / محمد حسين عبدالمقصود بشار

ملاحظات :

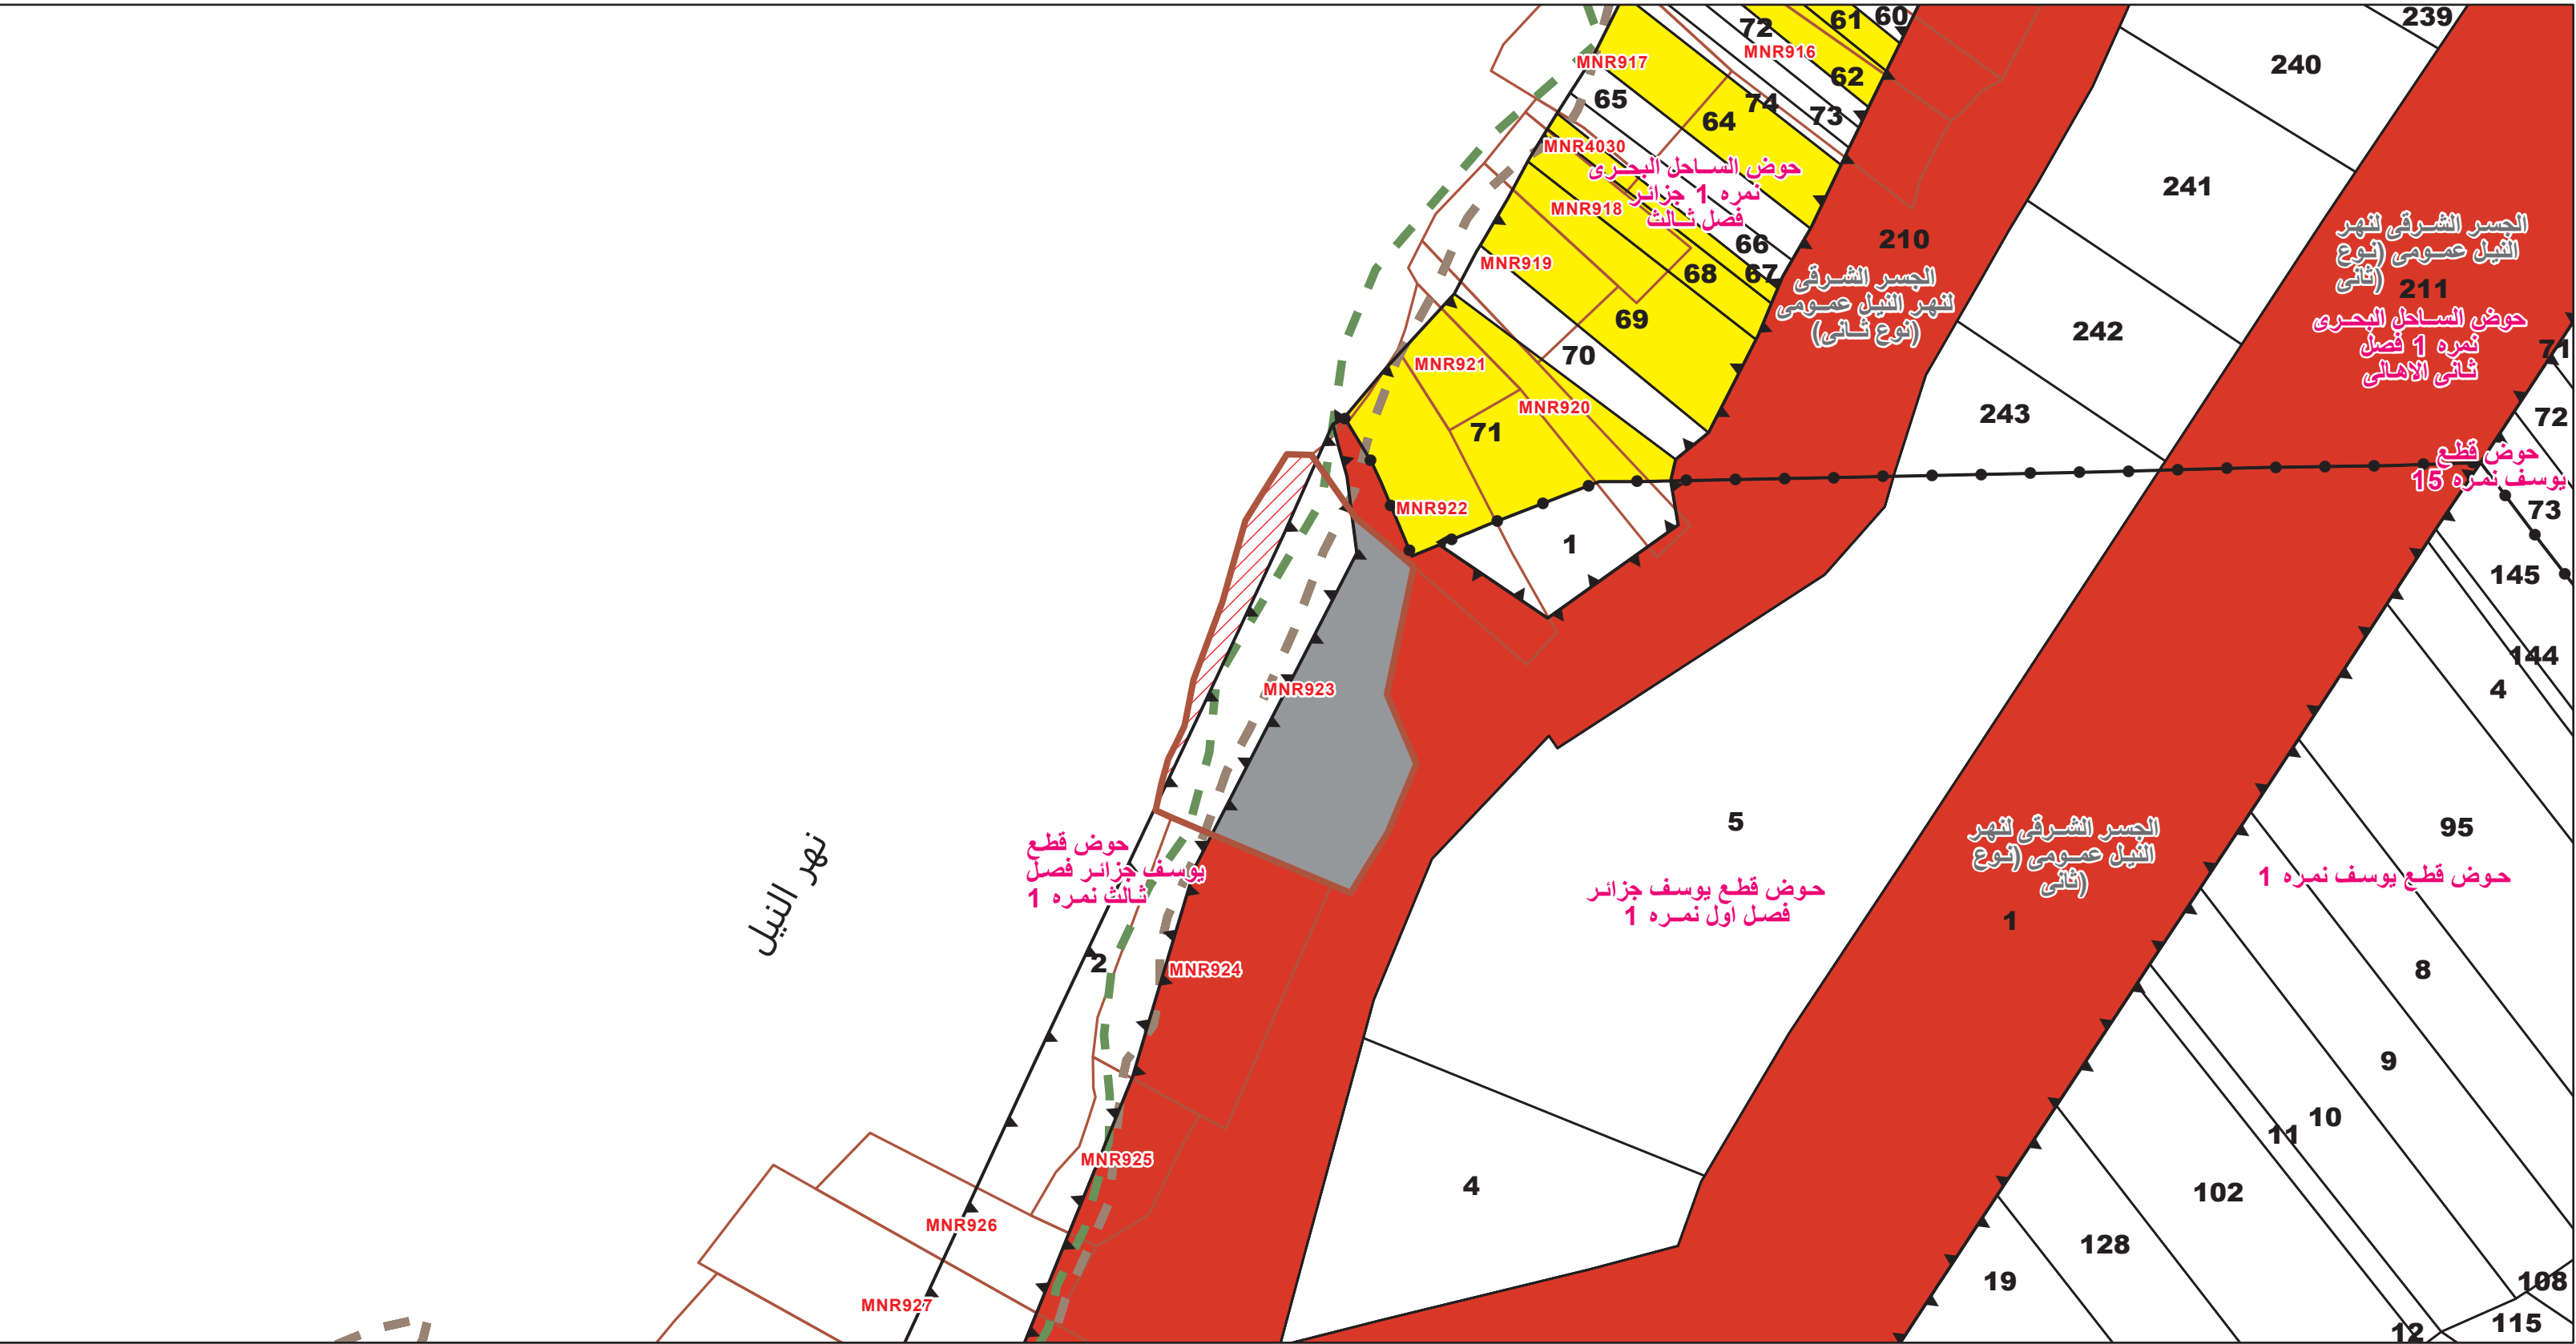

جدول بيانات املاك الدولة

جدول بيانات املاك الدولة															
		مسطح الاملاك				مسطح استثمارة 300									
الرمز	اسم القرية / المدينة	اسم الحوض	رقم القطعة	اسم المالك	اسم الجهة	س	ط	ف	م 2	س	ط	ف	م 2	موقف الاملاك	مسطح الجزء المتداخل بالتواجد م2
MNR923				طبقا للقانون رقم 147 لسنة 2021م بإصدار قانون الموارد المائية و الري في المادة الثانية الفقرة رقم 1 هي املاك دولة	املاك اميرية				21.1	0	0		153.89		153.89

تمت أعمال الرفع المساحي للوحدات طبقا لقرار اللجنة رقم 198 لسنة 2023م
(اللجنة الفنية القانونية المالية لأستلام جميع الاراضي والعقارات والبيانات
المائية والري بموجب القانون رقم 147 لسنة 2021م وبارشاد ممثلي إدارته
تم إدراج تجزئات أراضي طرح النهر طبقا لما هو وارد من مديرية المياه

تم تحديد قطع الاملاك وإدراج مسطحاتها بناءً على البحث الوارد من مصلحة الشهر العقاري أراضي خارج الحياض طبقاً لبحث الشهر العقاري هي طرح نهر املاك دولة وفقاً للقانون رقم 147 لسنة 2021 م بصدار قانون الموارد المائية و الري في المادة الثانية الفقرة رقم 1