

المدينة / القرية : مدينة طلخا

حوض الساحل الشرقي نمرة 36 جزاير فصل ثانی / حوض الساحل الشرقي نمرة 36 جزاير فصل ثالث

رقم الموقع : TAL0723

اسم المنتفع : / نادي المهندسين

ملاحظات :

جمهورية مصر العربية

وزارة الموارد المائية و الري

الهيئة المصرية العامة للمساحة



EGYPTIAN SURVEY AUTHORITY

أنتجت بمعرفة : الادارة المركزية للسجل العيني

بناءً على البيانات الواردة من مديرية المساحة

جدول مسطحات التواجد بالمتر المربع

5542.68	إجمالي مسطح التواجد
162.34	مسطح الاراضي خارج الحياض
	مسطح التعدي علي جسر نهر النيل
	مسطح التعدي علي المنافع العامة
	مسطح التعدي علي الشارع
	مسطح المنشآت داخل التواجد
0.00	مسطح الردم واجب ازالته طبقا لخرائط معهد البحوث لسنة 1982م
0.00	مسطح الردم واجب ازالته طبقا لخرائط معهد البحوث لسنة 2003م

لاحداثيات الخاصة بالموقع طبقا للاحداثي العالمي WGS_1984_UTM_Zone_36N

N	E	رقم الموقع
31° 3' 12.681" N	31° 23' 30.322" E	TAL0723


لرموز و الاصطلاحات المساحية

نقطة اعدادي	
حد الملكية	
حد حوض	
حد قرية	
خط التهذيب طبقا لاحداثيات معهد بحوث النيل خرائط 1982 م	
خط موازي لخط التهذيب 1982 م على بعد 30 م	
خط موازي لجسر نهر النيل على مسافة 30م	
خط الشاطئ طبقا لاحداثيات معهد بحوث النيل خرائط 1982م	
خط الشاطئ طبقا لاحداثيات معهد بحوث النيل خرائط 2003م	
اراضي الرفع بالطبيعة (التواجدات)	
مبانى رفع بالطبيعة	
تجزئات تاريخية	
تجزئات مؤقتة	
جسر نهر النيل	
الطــــــــــــرق	
مشروعات المنفعة العامة (السري)	
مشروعات المنفعة العامة (الصرف)	
مشروعات المنفعة العامة (اخرى)	
املاك الاوقاف	
املاك امــــــــــــيرية	
اصلاح زراــــــــعــــــــى	
تأشيرة تحفــــــــظ	
املاك اخــــــــــــري	
حد مركز	
حد محافظة	
حد نهر النيل	

الواجهة على النيل

162.89

نقطة احداثي

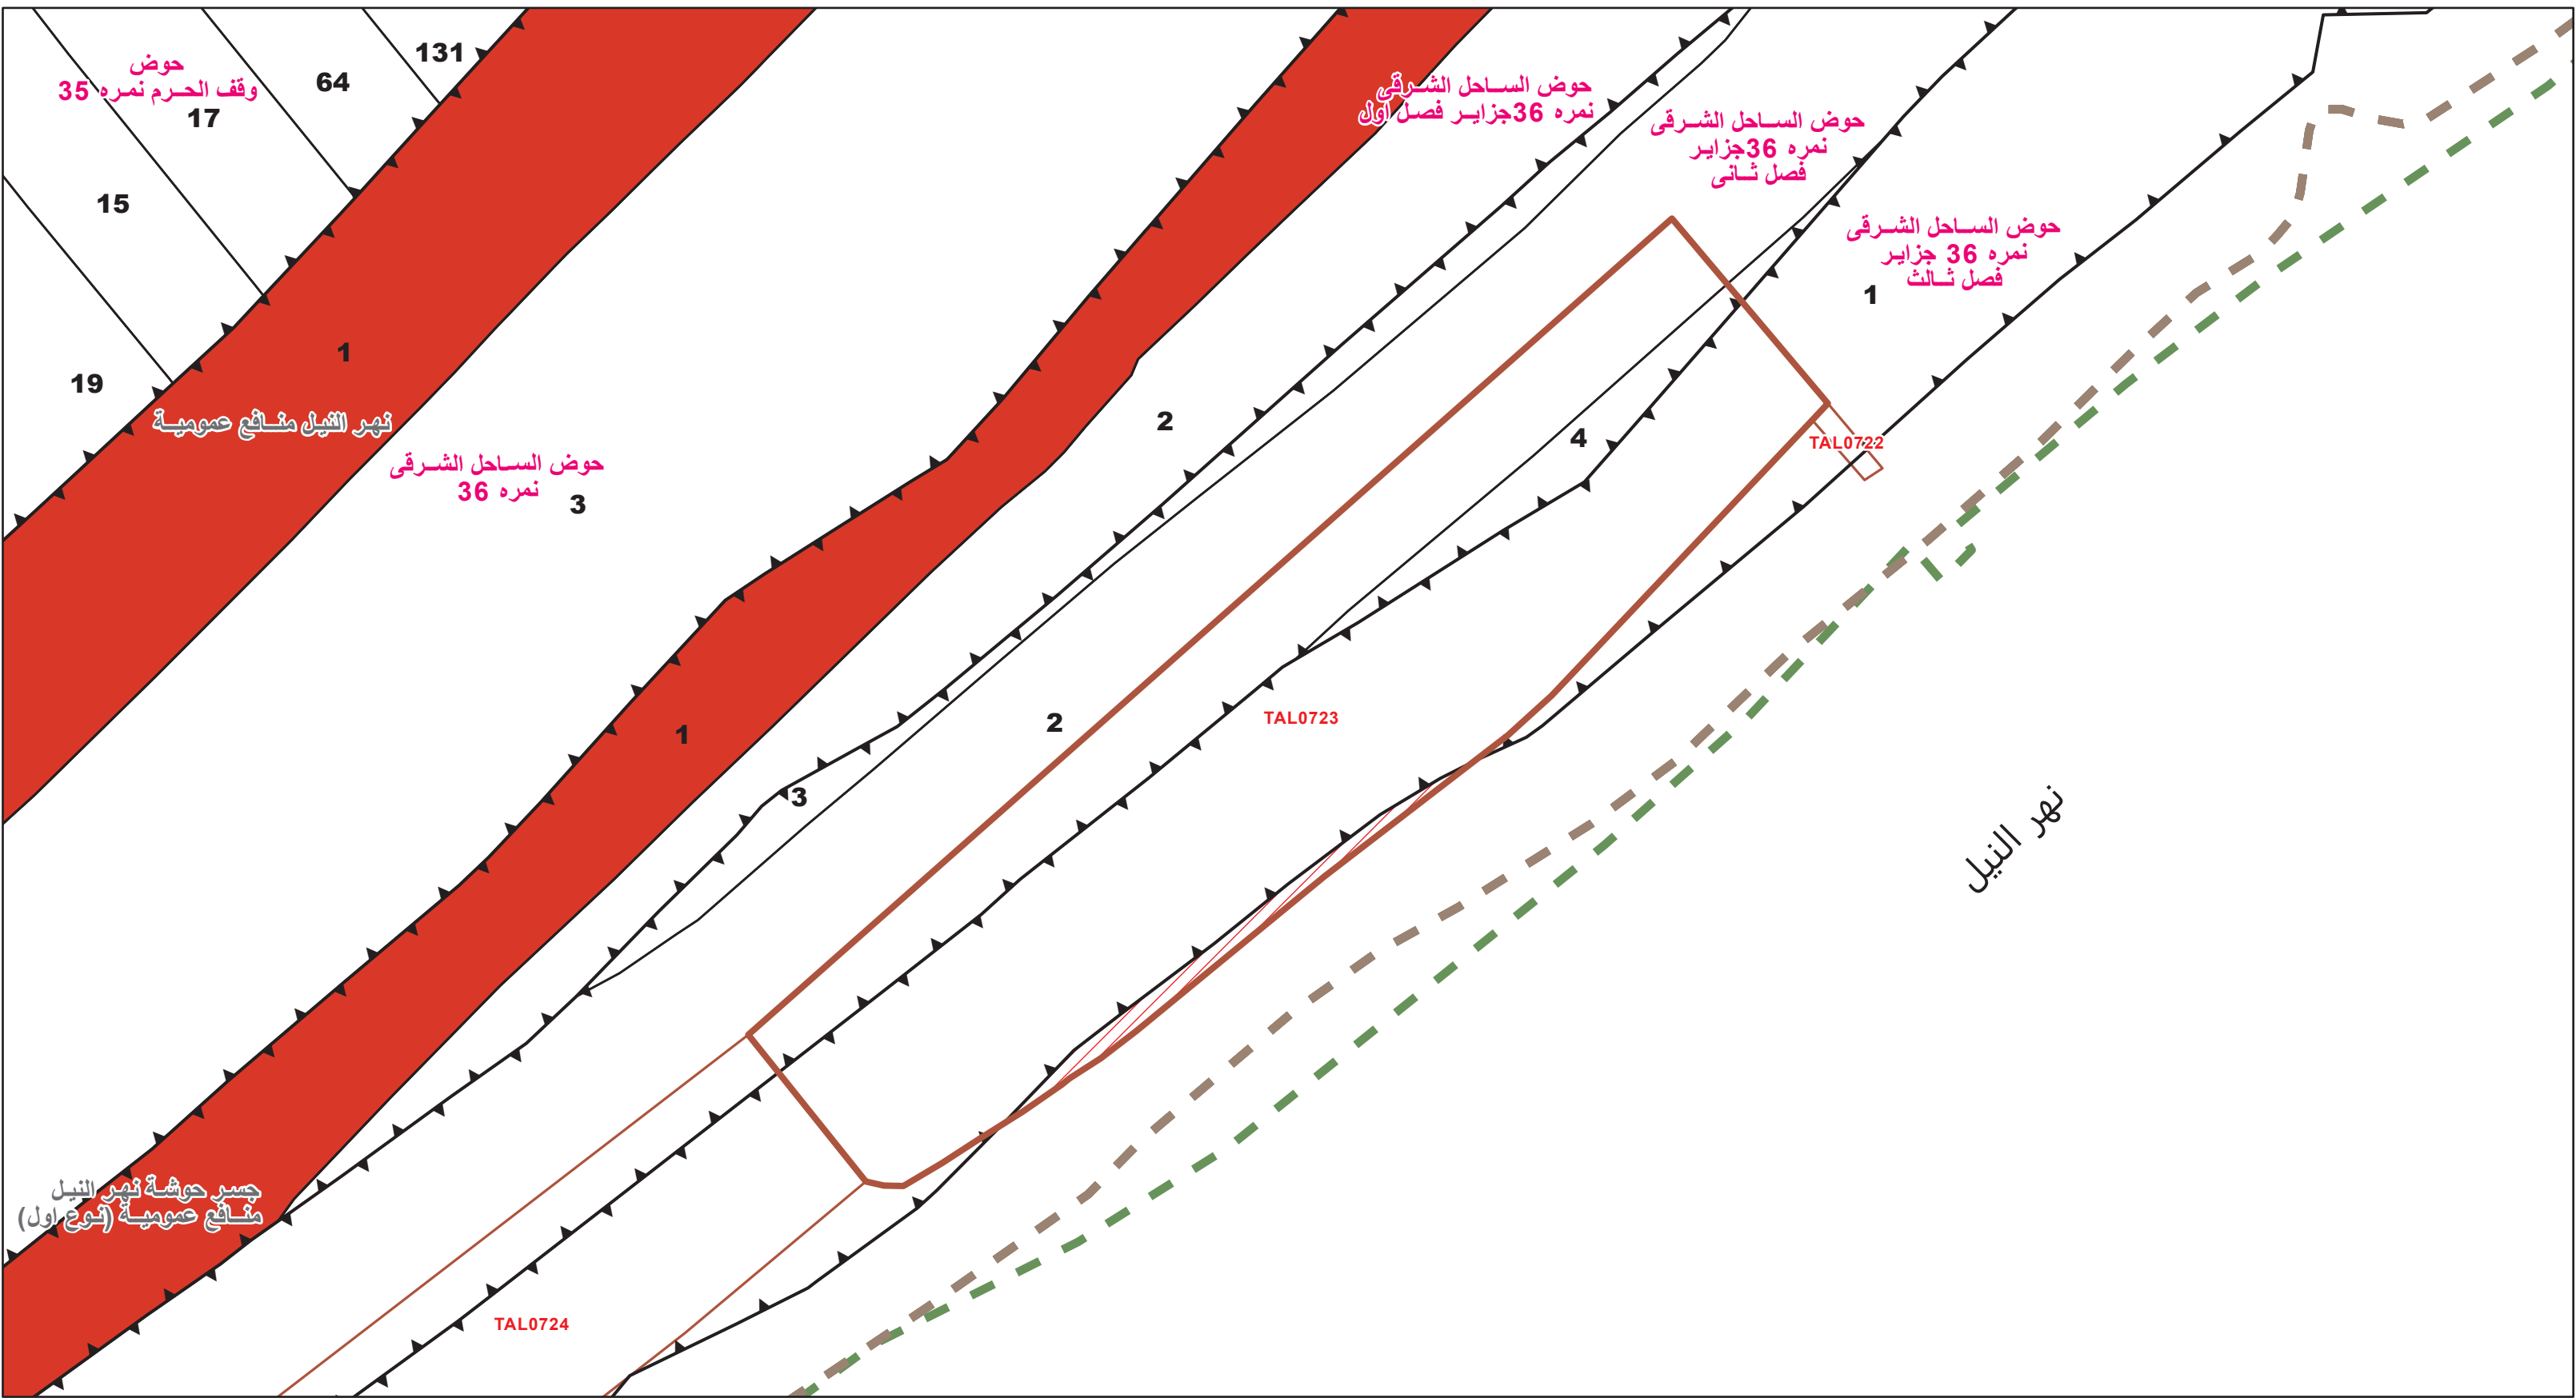

جدول بيانات املاك الدولة

جدول بيانات املاك الدولة															
		مسطح الاملاك				مسطح استثمارة 300									
الرمز	اسم القرية / المدينة	اسم الحوض	رقم القطعة	اسم المالك	اسم الجهة	س	ط	ف	م 2	س	ط	ف	م 2	موقف الاملاك	مسطح الجزء المتداخل بالتواجد م2
TAL0723				طبقا للقانون رقم 147 لسنة 2021م بإصدار قانون الموارد المائية و الري في المادة الثانية الفقرة رقم 1 هي املاك دولة	املاك اميرية					22.3	0	0	162.34		162.34