

المحافظة : الدقهلية
المركز : طلخا
حوض السكه الحديد والبلتاجى نمرة 31 / حوض السكه الحديد والبلتاجى نمرة31 جزاير فصل ثالث

المدينة / القرية : مدينة طلخا


تاريخ الطباعة : 31-03-2026

رقم الموقع : TAL0741

اسم المتنفع : / حديقة عروس النيل

ملاحظات :

تمت أعمال الرفع المساحي للتواجدات طبقا لقرار اللجنة رقم 198 لسنة 2023م
(اللجنة الفنية القانونية المالية لاستلام جميع الاراضي والعقارات والبيقات . والمستندات الخاصة بالاراضي التي الت ولايتها .وزارة الموارد المائية والري بموجب القانون رقم 147 لسنة 2021وبإرشاد ممثلي إدارة عملية النيل - هيئة التسيير و التنمية الزراعية - الاصلاح الزراعي تم إدراج تجزئات أراضي طرح النهر طبقا لما هو وارد من مديرية المساحة)
تم تحديد قطع الاملاك وإدراج مسطحاتها بناءاً علي البحث الوارد من مصلحة الشهر العقاري
أراضي خارج الحياض طبقاً لبحث الشهر العقاري هي طرح نهر أملاك دولة وفقاً للقانون رقم 147 لسنة 2021 م بإصدار قانون الموارد المائية و الري في المادة الثانية الفقرة رقم 1

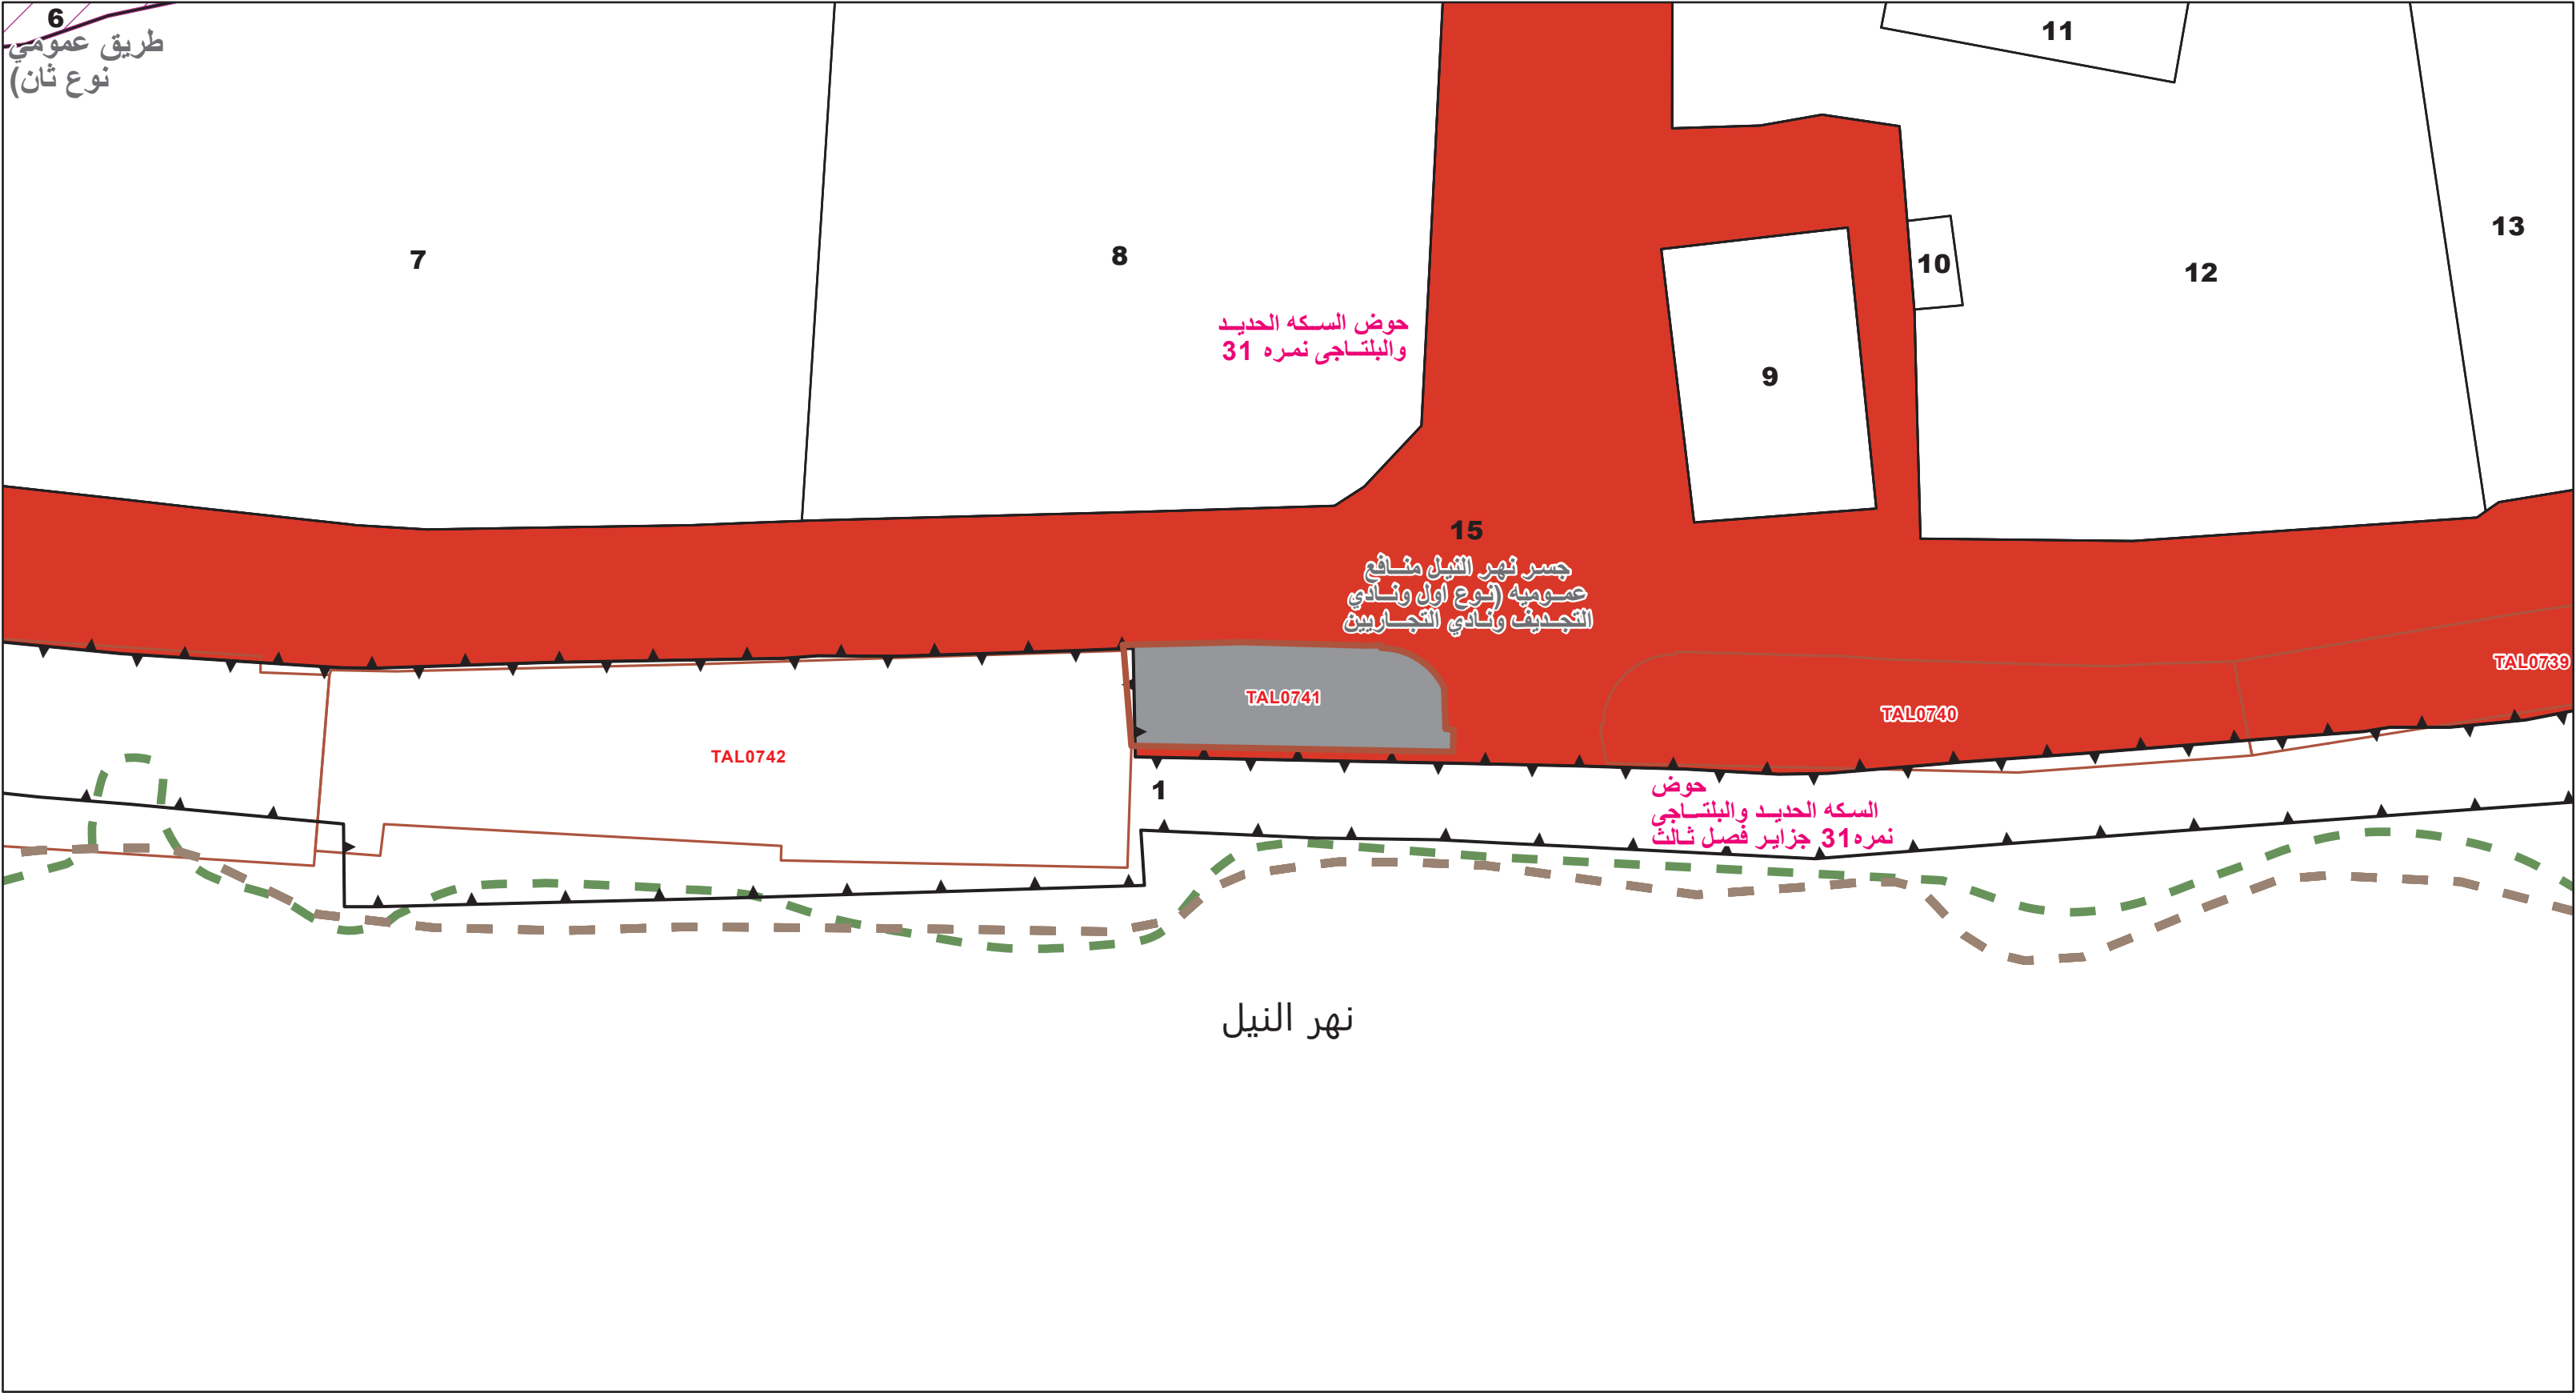

جدول بيانات املاك الدولة										الرمز	اسم القرية / المدينة	اسم الحوض	رقم القطعة	اسم المالك	اسم الجهة	مسطح استمارة 300				مسطح الاملاك				موقف الاملاك	مسطح الجزء المتداخل بالتواجد م2
س	ط	ف	م	س	ط	ف	م	س	ط	ف	م	س	ط	ف	م	س	ط	ف	م	س	ط	ف	م	موقف الاملاك	مسطح الجزء المتداخل بالتواجد م2

جمهورية مصر العربية
وزارة الموارد المائية و الري
الهيئة المصرية العامة للمساحة

EGYPTIAN SURVEY AUTHORITY

أنتجت بمعرفة : الادارة المركزية للسجل العيني

بناءاً على البيانات الواردة من مديرية المساحة

جدول مسطحات التواجد بالمتر المربع

إجمالي مسطح التواجد	568.65
مسطح الاراضي خارج الحياض	
مسطح التعدي علي جسر نهر النيل	557.26
مسطح التعدي علي المنافع العامة	
مسطح التعدي علي الشارع	
مسطح المنشآت داخل التواجد	
مسطح الردم واجب إزالته طبقا لخرائط معهد البحوث لسنة 1982م	0.00
مسطح الردم واجب إزالته طبقا لخرائط معهد البحوث لسنة 2003م	0.00

الاحداثيات الخاصة بالموقع طبقا لاحداثي العالمي WGS_1984_UTM_Zone_36N

رقم الموقع	E	N
TAL0741	31° 22' 47.472" E	31° 2' 59.153" N

الرموز و الاصطلاحات المساحية

نقطة احداثي

حد الملكية

حد حوض

حد قرية

خط التهذيب طبقا لاحداثيات معهد بحوث النيل خرائط 1982 م

خط موازي لخط التهذيب1982 م على بعد 30 م

خط موازي لجسر نهر النيل على مسافة 30م

خط الشاطئ طبقا لاحداثيات معهد بحوث النيل خرائط 1982م

خط الشاطئ طبقا لاحداثيات معهد بحوث النيل خرائط 2003م

اراضي الرفع بالطبيعة (التواجدات)

مبانى رفع بالطبيعة

تجزئات تاريخية

تجزئات مؤقتة

جسر نهر النيل

الطريق

مشروعات المنفعة العامة (الري)

مشروعات المنفعة العامة (الصرف)

مشروعات المنفعة العامة (اخرى)

حد مركز

حد محافظة

حد نهر النيل

ارضى خارج الحياض (ارساب)

التعدي علي المنفعة العامة

التعدي علي جسر نهر النيل

الردم لسنة 1982م

مبانى رفع القوات المسلحة

املاك الاوقاف

املاك امميرية

اصلاح زراعى

تأشيرة تحفظ

املاك اخصري

طول الواجهة علي النيل

42.53

TAL0741

نقطة احداثي