


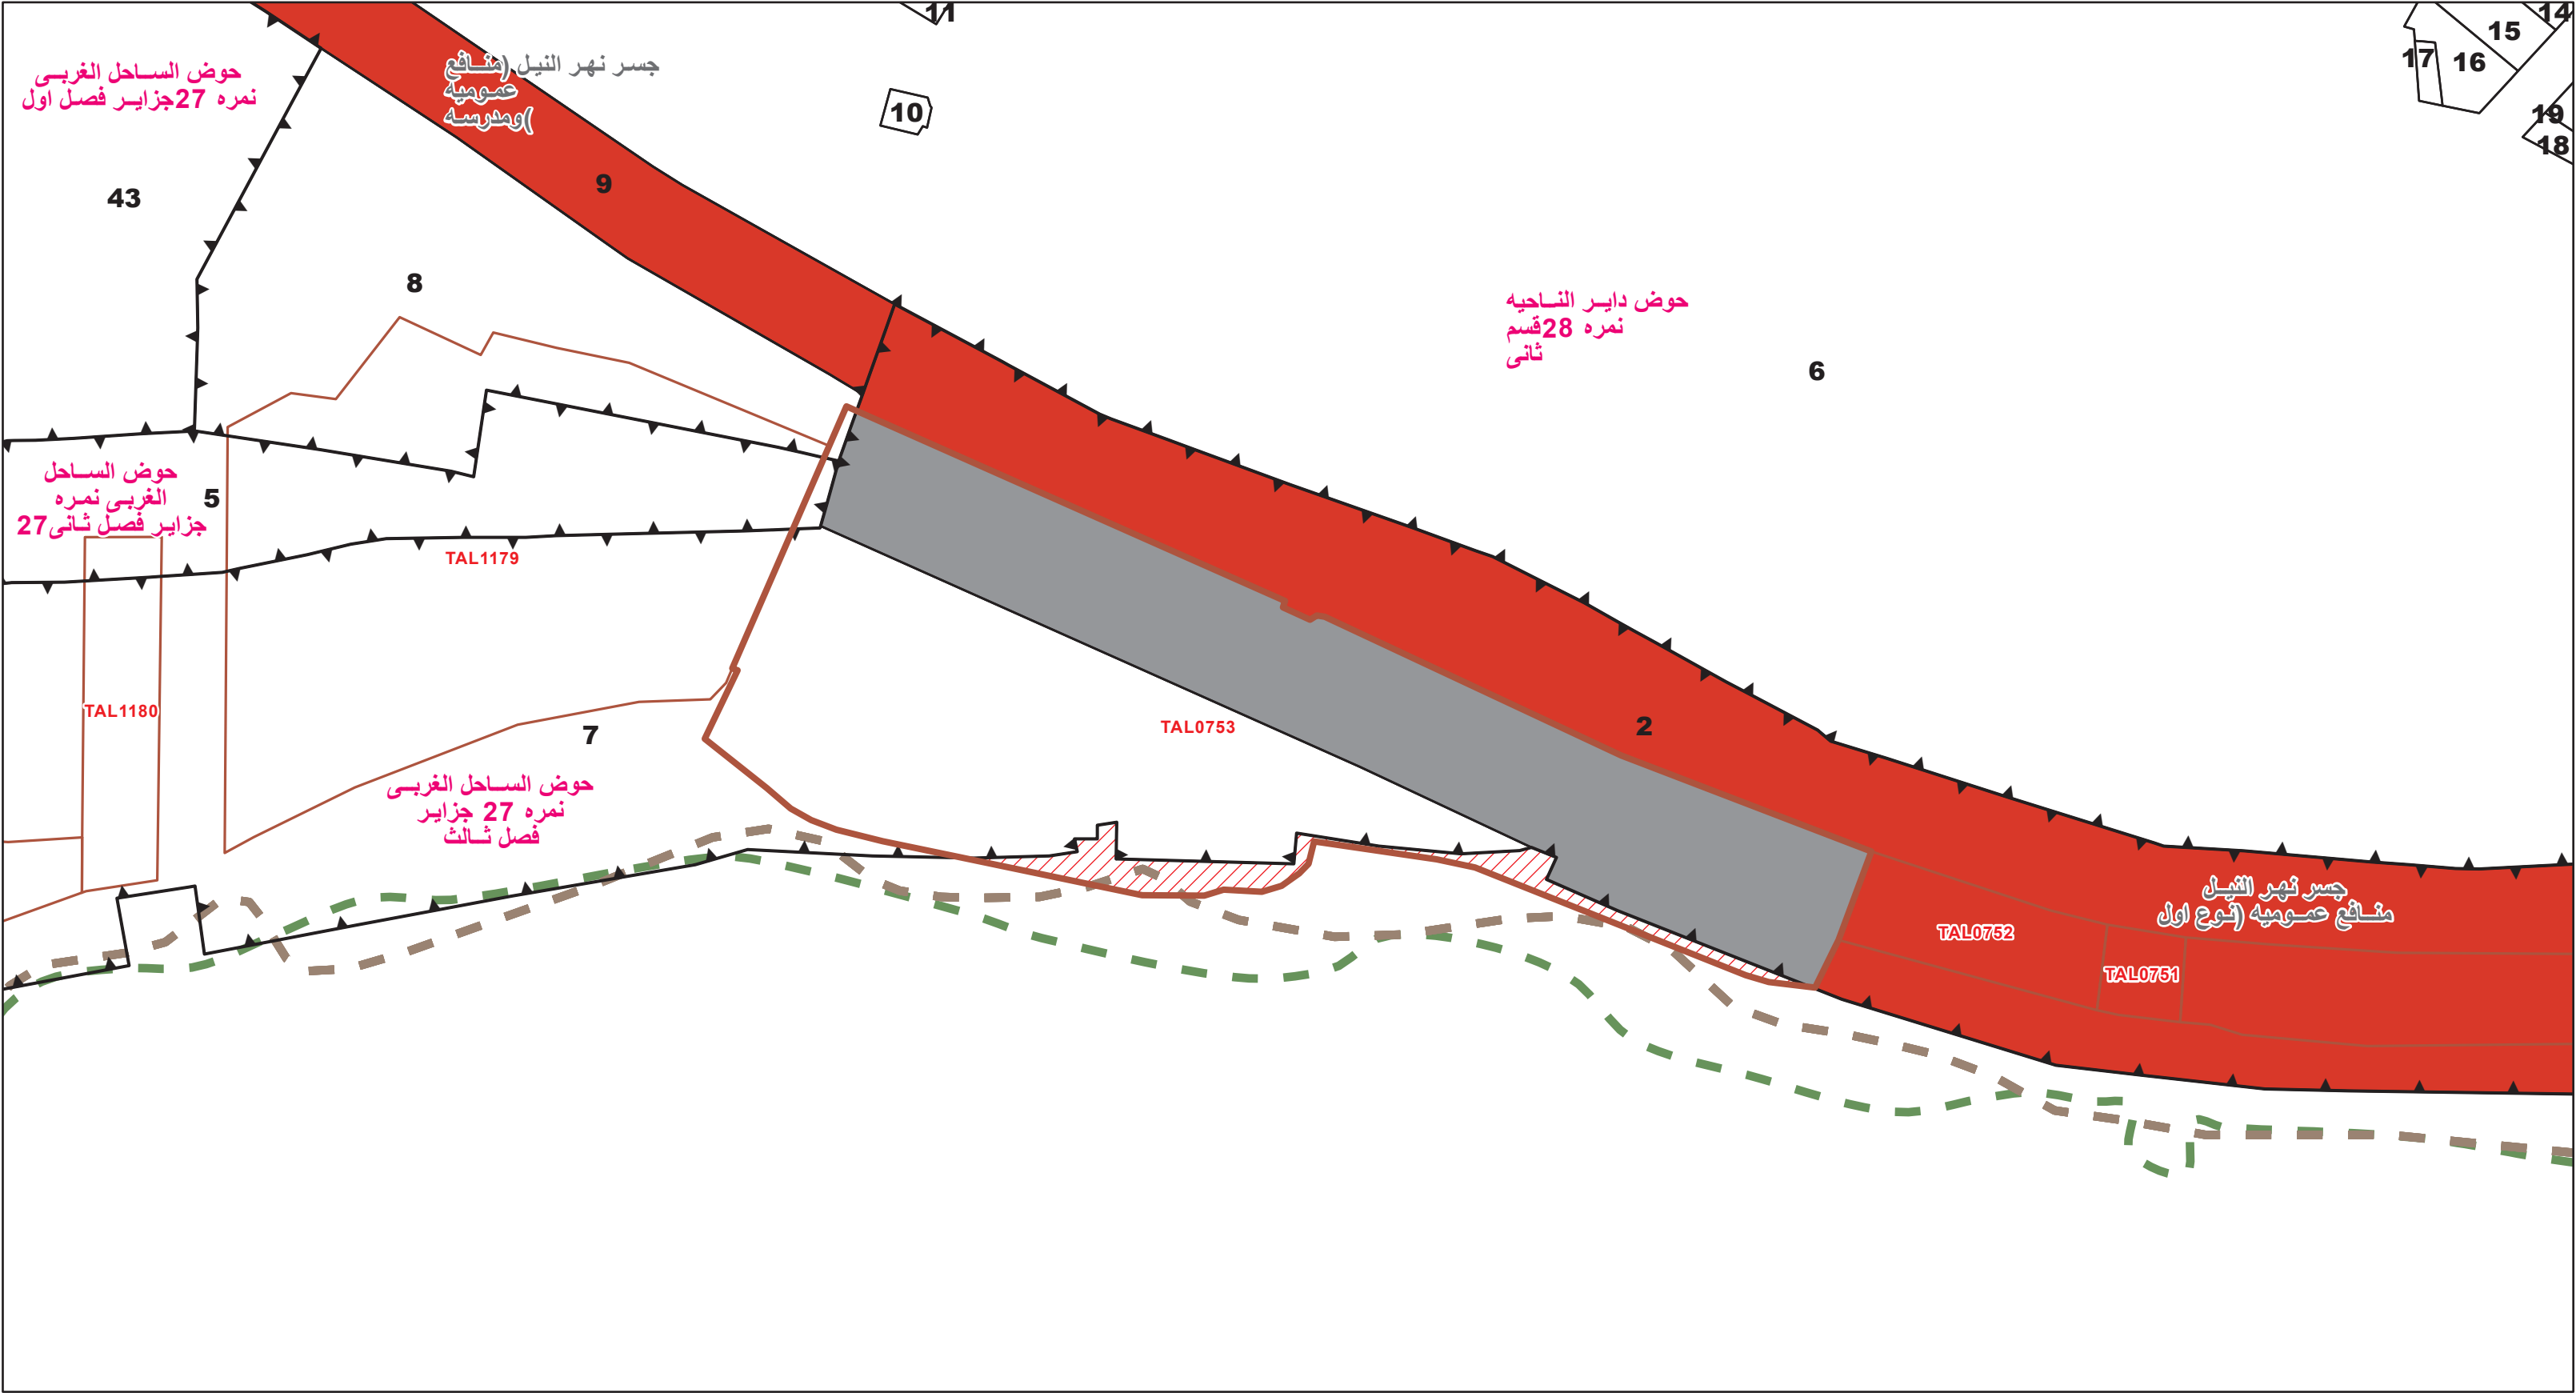

جدول بيانات املاك الدولة															
		مسطح استمارة 300				مسطح الاملاك									
الرمز	اسم القرية / المدينة	اسم الحوض	رقم القطعة	اسم المالك	اسم الجهة	س	ط	ف	م 2	س	ط	ف	م 2	موقف الاملاك	مسطح الجزء المتداخل بالتواجد م2
TAL0753				طبقا للقانون رقم 147 لسنة 2021م بإصدار قانون الموارد المائية و الري في المادة الثانية الفقرة رقم 1 هي املاك دولة	املاك اميرية					15.6	1	0	288.53		288.53

جمهورية مصر العربية
وزارة الموارد المائية و الري
الهيئة المصرية العامة للمساحة

EGYPTIAN SURVEY AUTHORITY

أنتجت بمعرفة : الادارة المركزية للسجل العيني

بناءاً على البيانات الواردة من مديرية المساحة

جدول مسطحات التواجد بالمتر المربع

إجمالي مسطح التواجد	5195.91
مسطح الاراضي خارج الحياض	288.53
مسطح التعدي علي جسر نهر النيل	2460.13
مسطح التعدي علي المنافع العامة	
مسطح التعدي علي الشارع	
مسطح المنشآت داخل التواجد	
مسطح الردم واجب إزالته طبقا لخرائط معهد البحوث لسنة 1982م	22.23
مسطح الردم واجب إزالته طبقا لخرائط معهد البحوث لسنة 2003م	0.00

الاحداثيات الخاصة بالموقع طبقا للاحداثي العالمي WGS_1984_UTM_Zone_36N

رقم الموقع	E	N
TAL0753	31° 22' 20.461" E	31° 3' 0.407" N

الرموز و الاصطلاحات المساحية

نقطة احداثي

حد الملكية

حد حوض

حد قرية

خط التهذيب طبقا لاحداثيات معهد بحوث النيل خرائط 1982 م

خط موازي لخط التهذيب1982 م على بعد 30 م

خط موازي لجسر نهر النيل على مسافة 30م

خط الشاطئ طبقا لاحداثيات معهد بحوث النيل خرائط 1982م

خط الشاطئ طبقا لاحداثيات معهد بحوث النيل خرائط 2003م

اراضي الرفع بالطبيعة (التواجدات)

مياشي رفع بالطبيعة

تجزئات تاريخية

تجزئات مؤقتة

جسر نهر النيل

الطريق

مشروعات المنفعة العامة (الري)

مشروعات المنفعة العامة (الصرف)

مشروعات المنفعة العامة (اخرى)

حد مركز

حد محافظة

حد نهر النيل

خط التهذيب طبقا لاحداثيات معهد بحوث النيل خرائط 1982 م

خط موازي لخط التهذيب1982 م على بعد 30 م

خط موازي لجسر نهر النيل على مسافة 30م

خط الشاطئ طبقا لاحداثيات معهد بحوث النيل خرائط 1982م

خط الشاطئ طبقا لاحداثيات معهد بحوث النيل خرائط 2003م

اراضي خارج الحياض (ارساب)

التعدي علي المنفعة العامة

التعدي علي جسر نهر النيل

الردم لسنة 1982م

مياشي رفع القوات المسلحة

املاك الاوقاف

املاك اميرية

اصلاح زراعي

تأشيرة تحفظ

املاك اخصري

طول الواحية علي النيل

176.29

TAL0753

نقطة احداثي